

รายการสัญลักษณ์แบบ สารบัญแบบ และรายการประกอบแบบ



รายการสัญลักษณ์แบบ	
สัญลักษณ์	รายละเอียด
	สัญลักษณ์การบอกทิศเหนือ
	1. แสดงชื่อแบบขยาย 2. แสดงเลขที่แผ่น ที่แบบไปปรากฏ
	1. แสดงชื่อรูปตัด 2. แสดงเลขที่แผ่น ที่แบบไปปรากฏ
	1. แสดงชื่อห้อง 2. แสดงสัญลักษณ์พื้น 3. แสดงระดับพื้น 4. แสดงสัญลักษณ์ฝ้า
	แสดงแนวตัด
	① สัญลักษณ์แสดงแนวเสาดตามแนวตั้ง (ตัวอักษร) Ⓐ สัญลักษณ์แสดงแนวเสาดตามแนวนอน (ตัวเลข)
	สัญลักษณ์แสดงการบอกทิศทางการมองรูปด้าน
	สัญลักษณ์คอนกรีต
	แสดงผนังก่ออิฐฉาบปูน แสดงในแปลน
	แสดงผนังก่ออิฐฉาบปูน แสดงในรูปตัด
	แสดงผนังก่ออิฐบล็อดแก้ว แสดงในแปลน
	แสดงสัญลักษณ์ หน้าต่าง
	แสดงสัญลักษณ์ ประตู
	แสดงสัญลักษณ์ ฝ้าเพดาน
	แสดงสัญลักษณ์ ผนัง
	แสดงสัญลักษณ์ พื้น
	สัญลักษณ์ บอกระยะจากศูนย์กลาง ถึง ศูนย์กลาง
	สัญลักษณ์ บอกระยะจากศูนย์กลาง ถึง ริม
	สัญลักษณ์ บอกระยะจากริม ถึง ริม

เลขที่แบบ	แบบสถาปัตยกรรม
A-01	สารบัญแบบ, สัญลักษณ์แบบ, รายการประกอบแบบ
A-02	มาตรการรักษาความปลอดภัย
A-03	ผัง zon ดที่ดิน
A-04	แปลนพื้นที่ชั้นล่าง, แปลนหลังคา
A-05	รูปด้าน 1, รูปด้าน 2
A-06	รูปด้าน 3, รูปด้าน 4
A-07	รูปตัด A, รูปตัด B
A-08	แบบขยายประตู, แบบขยายหน้าต่าง
A-09	แบบขยายห้องน้ำ
เลขที่แบบ	แบบวิศวกรรมไฟฟ้า
EE-01	รายการประกอบแบบไฟฟ้า
EE-02	แปลนไฟฟ้า

เลขที่แบบ	แบบวิศวกรรมโครงสร้าง
S-01	สารบัญและรายการประกอบแบบ
S-02	รายละเอียดและข้อกำหนดทั่วไป 1
S-03	รายละเอียดและข้อกำหนดทั่วไป 2
S-04	รายละเอียดและข้อกำหนดทั่วไป 3
S-05	รายละเอียดและข้อกำหนดทั่วไป 4
S-06	รายละเอียดและข้อกำหนดทั่วไป 5
S-07	แปลนตำแหน่งฐานรากและเสาเข็ม
	แปลนคานชั้นล่าง
S-08	แปลนโครงหลังคาล่าง, แปลนโครงหลังคา
S-09	แบบขยายฐานราก F1-F2
S-10	แบบขยายเสา C1, CX, แบบขยายแผ่นเหล็กหัวเสา
S-11	มาตรฐานการเสริมเหล็กคาน
S-12	แบบขยายโครงสร้างคาน, พื้น, บันได
S-13	แบบขยายจุดต่อ "J1"
S-14	แบบขยายพื้นสำเร็จรูป
S-15	แบบขยายการเชื่อมโครงหลังคา 1
S-16	แบบขยายการเชื่อมโครงหลังคา 2
เลขที่แบบ	แบบสุขาภิบาล
SN-01	รายการสัญลักษณ์สุขาภิบาล
SN-02	แปลนสุขาภิบาล
SN-03	แบบขยายบ่อเกราะ-บ่อซึม
SN-04	แบบขยายบ่อพักสำเร็จรูป
	แบบขยายถังดักไขมัน และ การติดตั้ง

รายการประกอบแบบพื้น		
สัญลักษณ์	โครงสร้าง	รายละเอียดพื้น
F1	ค.ส.ล.	กระเบื้องขนาด 60x60 ซม. แกรนิตโต้
		พร้อมบัวเชิงผนังสำเร็จรูป (หรือเทียบเท่า)
F2	ค.ส.ล.	กระเบื้อง ขนาด 30x30 ซม.
รายการประกอบแบบผนัง		
สัญลักษณ์	โครงสร้าง	รายละเอียดผนัง
A1	อิฐมวลเบา ความหนา7.5ซม.	ฉาบปูนเรียบทาสีอะคริลิค
A2	อิฐมวลเบา ความหนา7.5ซม.	ปูกระเบื้อง ขนาด 30x30 ซม. สูงจรดฝ้าเพดาน
รายการประกอบแบบฝ้าเพดาน		
สัญลักษณ์	โครงสร้าง	รายละเอียดฝ้าเพดาน
C1	เหล็กชุบสังกะสี	ยิปซัมบอร์ดหนา 9 มม.ฉาบเรียบทาสี
C2	เหล็กชุบสังกะสี	ยิปซัมบอร์ดหนา 9 มม.(ชนิดทนชื้น) ฉาบเรียบทาสี
C3	เหล็กชุบสังกะสี	ฝ้าภายนอกสมาร์ทบอร์ดหนา 4 มม. ทาสี

PROJECT NAME						
สำนักงานนิติบุคคลหมู่บ้านจัดสรร พฤษภา 33						
LOCATION						
ตำบลบางแม่นาง						
อำเภอบางใหญ่ จังหวัดนนทบุรี						
OWNER						
นิติบุคคลหมู่บ้านจัดสรรพฤษภา33						
ARCHITECTS						
-						
-						
-						
ENGINEERS						
TITLE						
รายการสัญลักษณ์แบบ, สารบัญแบบ						
รายการประกอบแบบ						
REVISION						
1	2	3	4	5	6	7
DRAWN BY						
-						
.						
DATE	2025-09-01					
DRAWING NO.	TOTAL					
A-01	OF					

  


ตามประกาศ กรุงเทพมหานคร ลงวันที่ 23 กันยายน 2539


ฟังก์ชันกระจาย





PROJECT NAME						
สำนักงานนิติบุคคลหมู่บ้านจัดสรร พฤษภา 33						
LOCATION						
ตำบลบางแม่นาง						
อำเภอบางใหญ่ จังหวัดนนทบุรี						
OWNER						
นิติบุคคลหมู่บ้านจัดสรรพฤษภา33						
ARCHITECTS						
-						
-						
-						
ENGINEERS						
TITLE						
ข้อกำหนดในการก่อสร้าง						
มาตรการป้องกันเหตุเดือดร้อน						
REVISION						
1	2	3	4	5	6	7
DRAWN BY						
-						
.						
DATE	2025-09-01					
DRAWING NO.	TOTAL					
A-02	OF					

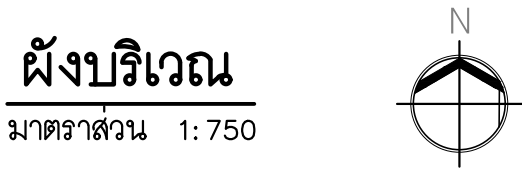


PROJECT NAME						
สำนักงานนิติบุคคลหมู่บ้านจัดสรร พฤษภา 33						
LOCATION						
ตำบลบางแม่นาง						
อำเภอบางใหญ่ จังหวัดนนทบุรี						
OWNER						
นิติบุคคลหมู่บ้านจัดสรรพฤษภา33						
ARCHITECTS						
-						
-						
-						
ENGINEERS						
-						
-						
-						
TITLE						
ผังบริเวณ						
-						
REVISION						
1	2	3	4	5	6	7
DRAWN BY						
-						
.						
DATE	2025-09-01					
DRAWING NO.	TOTAL					
A-03	OF					

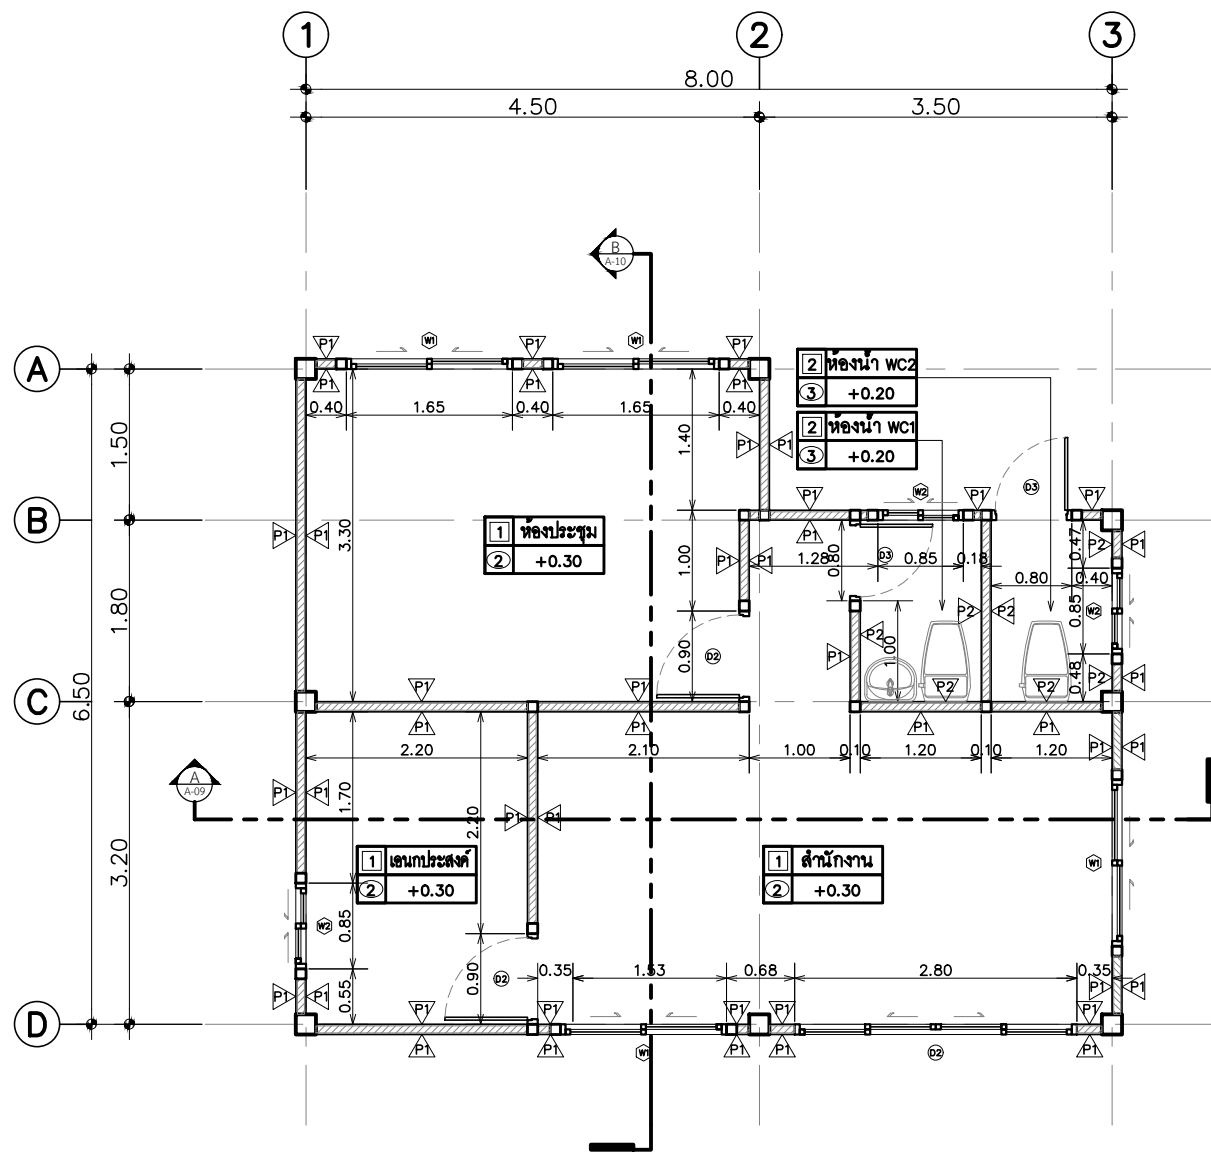


แปลนพื้น
มาตราส่วน 1: 75

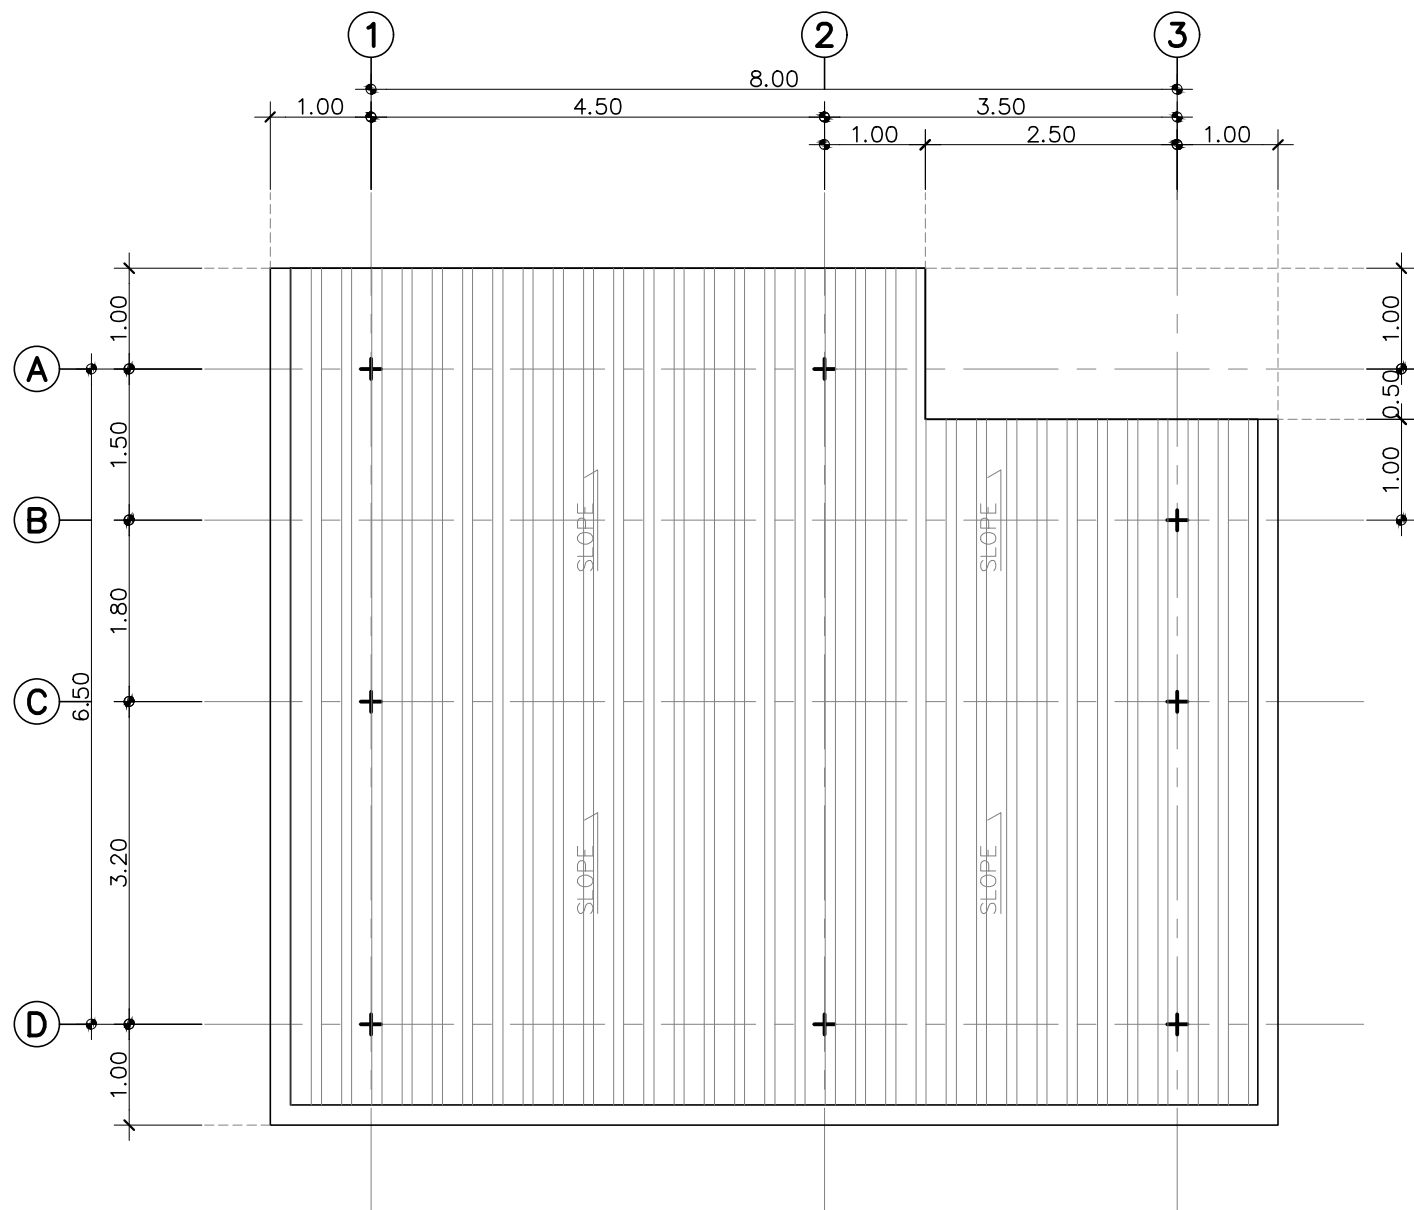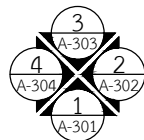


แปลนหลังคา
มาตราส่วน 1: 75

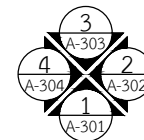

PROJECT NAME						
สำนักงานนิติบุคคลหมู่บ้านจัดสรร ทฤษฎา 33						
LOCATION						
ตำบลบางแม่นาง						
อำเภอบางใหญ่ จังหวัดนนทบุรี						
OWNER						
นิติบุคคลหมู่บ้านจัดสรรทฤษฎา33						
ARCHITECTS						
-						
-						
-						
ENGINEERS						
-						
-						
-						
TITLE						
แปลนพื้น						
แปลนหลังคา						
REVISION						
1	2	3	4	5	6	7
DRAWN BY						
-						
.						
DATE	2025-09-01					
DRAWING NO.	TOTAL					
A-04	OF					

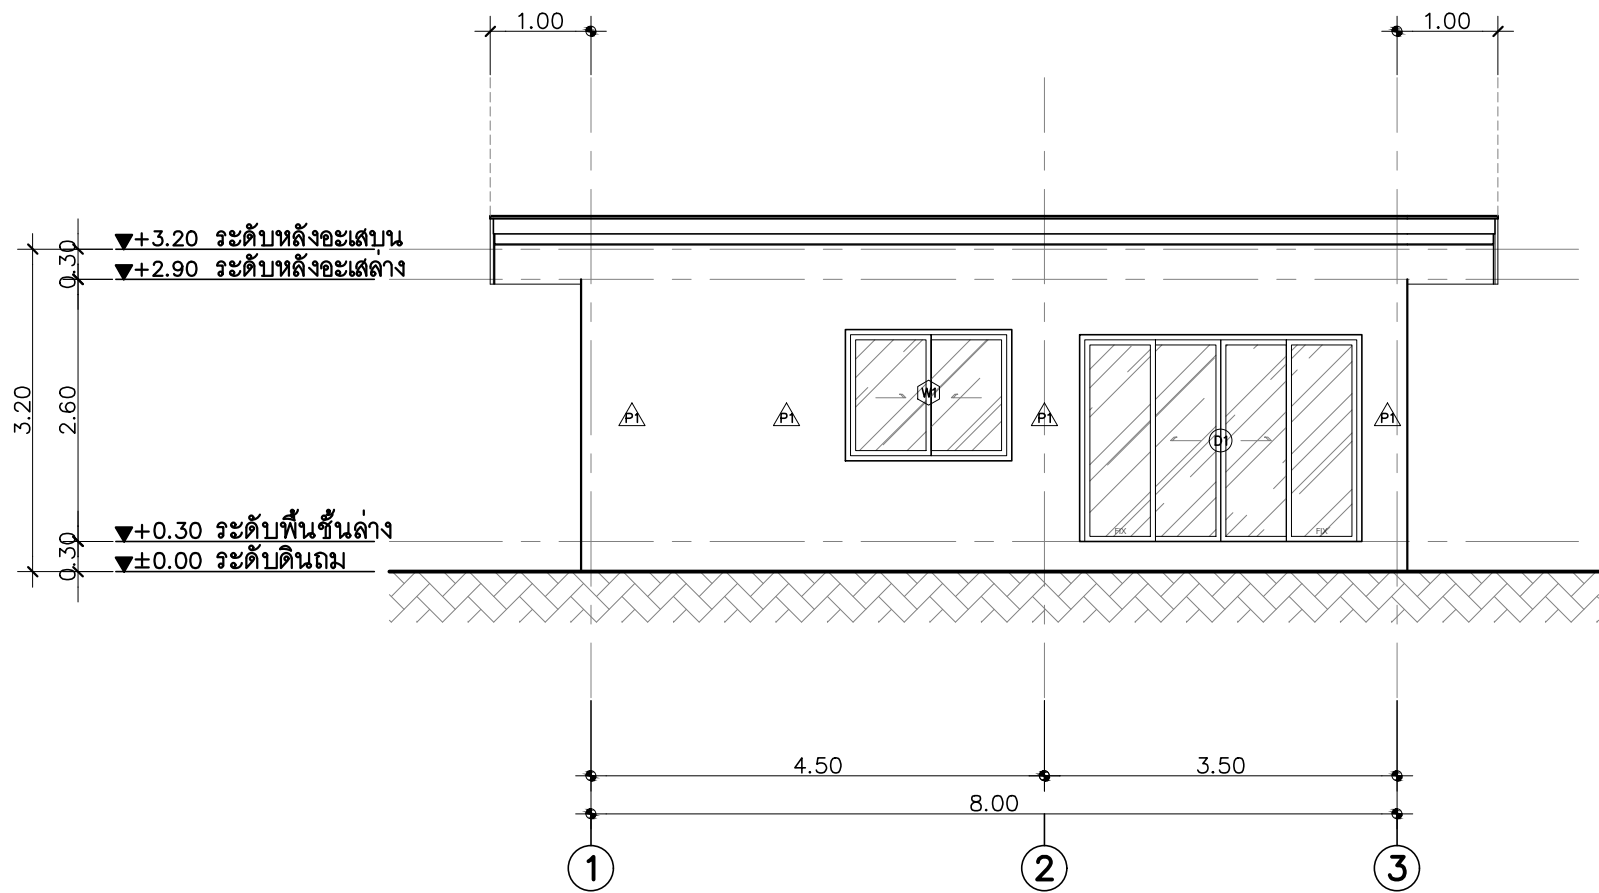


รูปด้าน 1
มาตราส่วน 1: 75

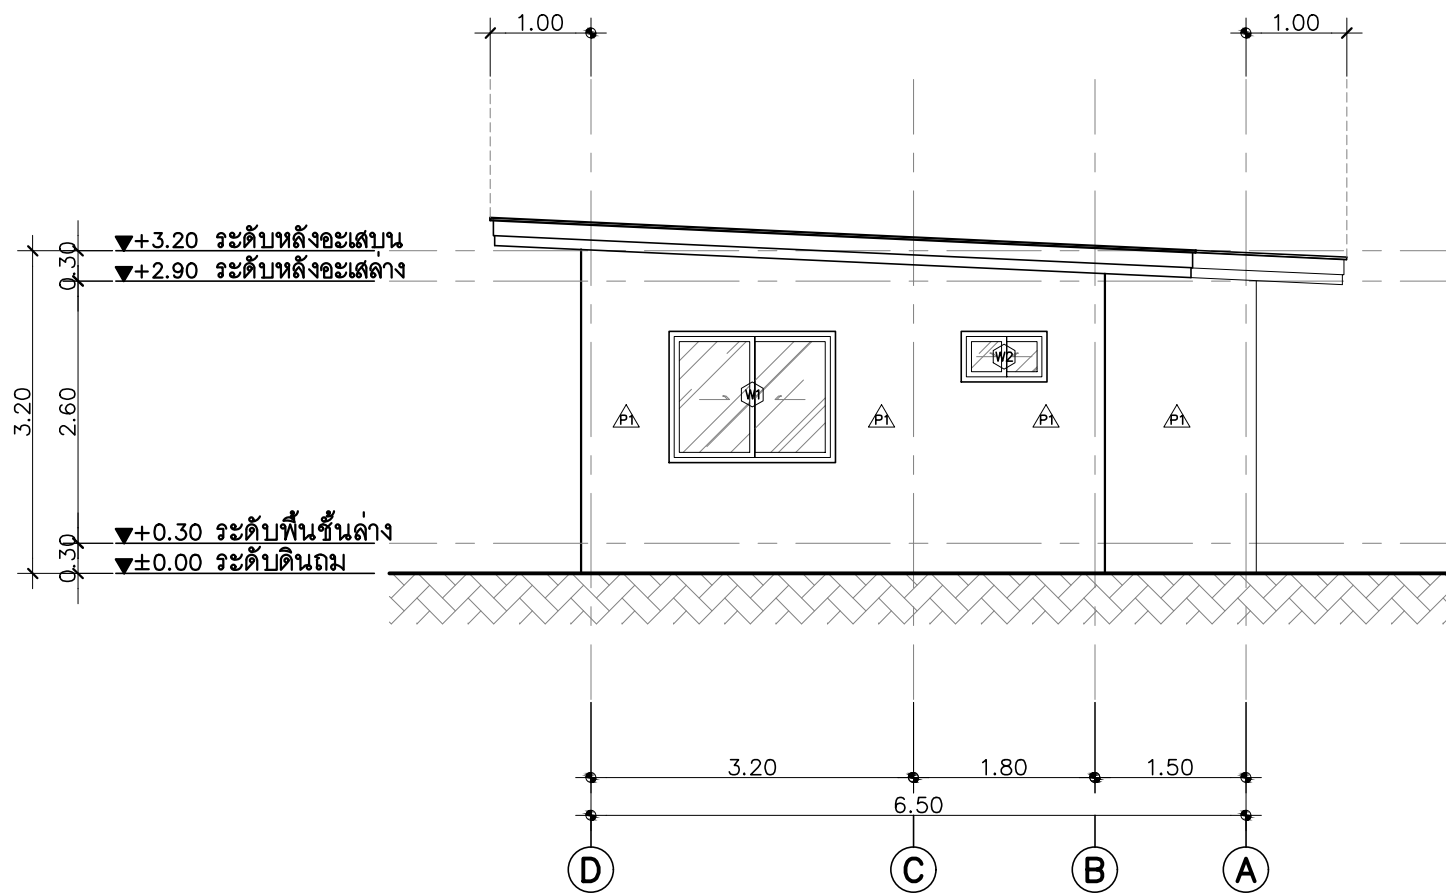


รูปด้าน 2
มาตราส่วน 1: 75

PROJECT NAME						
สำนักงานนิติบุคคลหมู่บ้านจัดสรร ทฤษฎา 33						
LOCATION						
ตำบลบางแม่นาง						
อำเภอบางใหญ่ จังหวัดนนทบุรี						
OWNER						
นิติบุคคลหมู่บ้านจัดสรรทฤษฎา33						
ARCHITECTS						
-						
-						
-						
ENGINEERS						
-						
-						
-						
TITLE						
รูปด้าน 1						
รูปด้าน 2						
REVISION						
1	2	3	4	5	6	7
DRAWN BY						
-						
.						
DATE	2025-09-01					
DRAWING NO.	TOTAL					
A-05	OF					

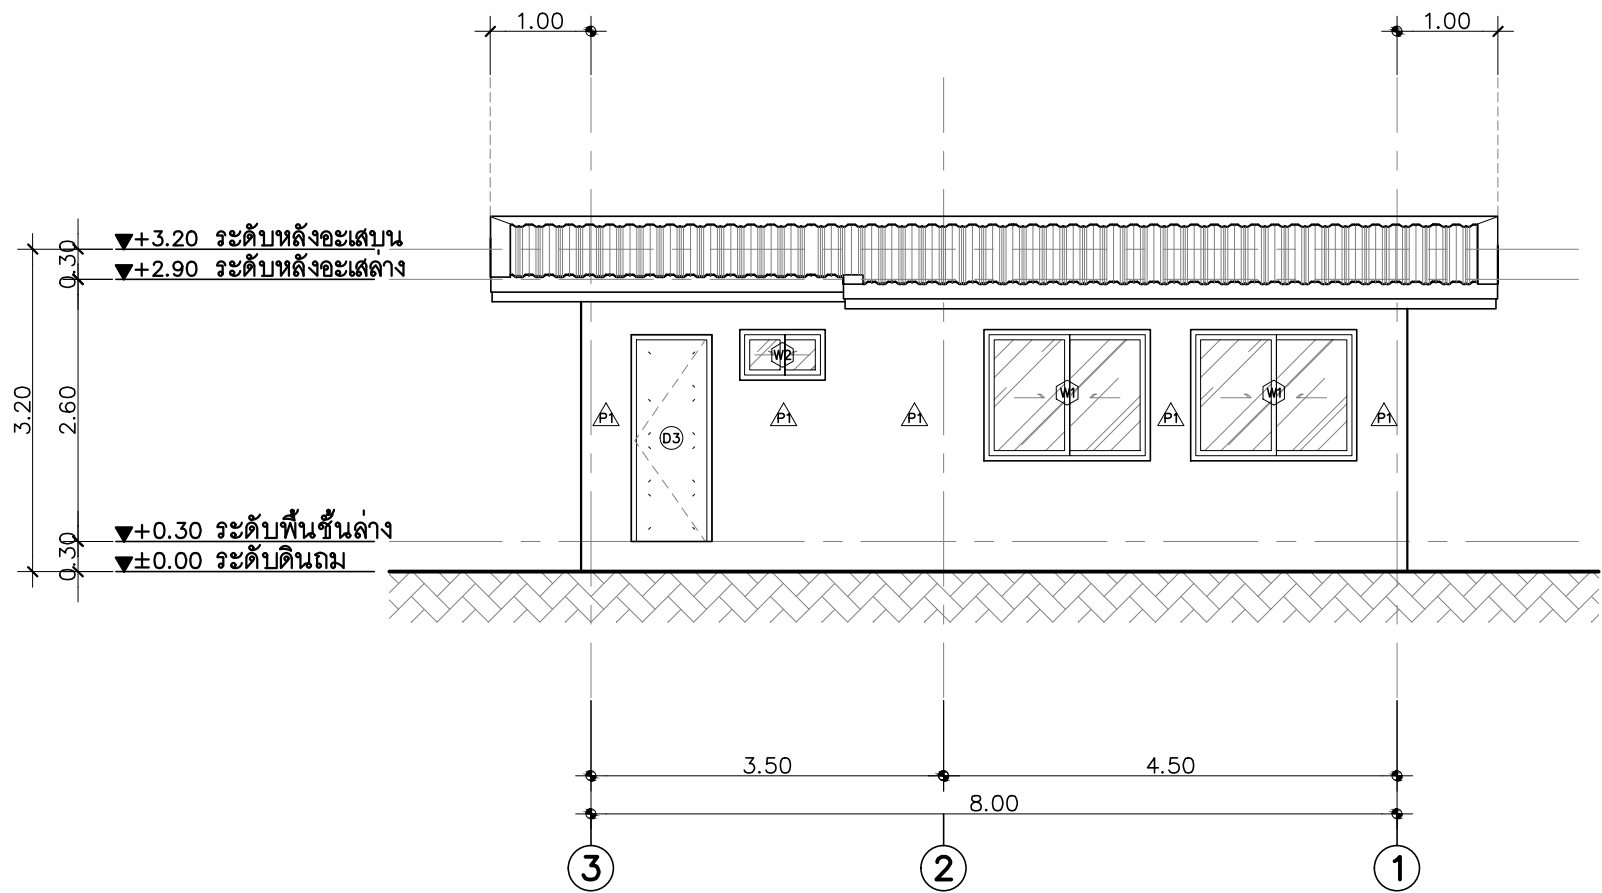


รูปด้าน 2
มาตราส่วน 1: 75

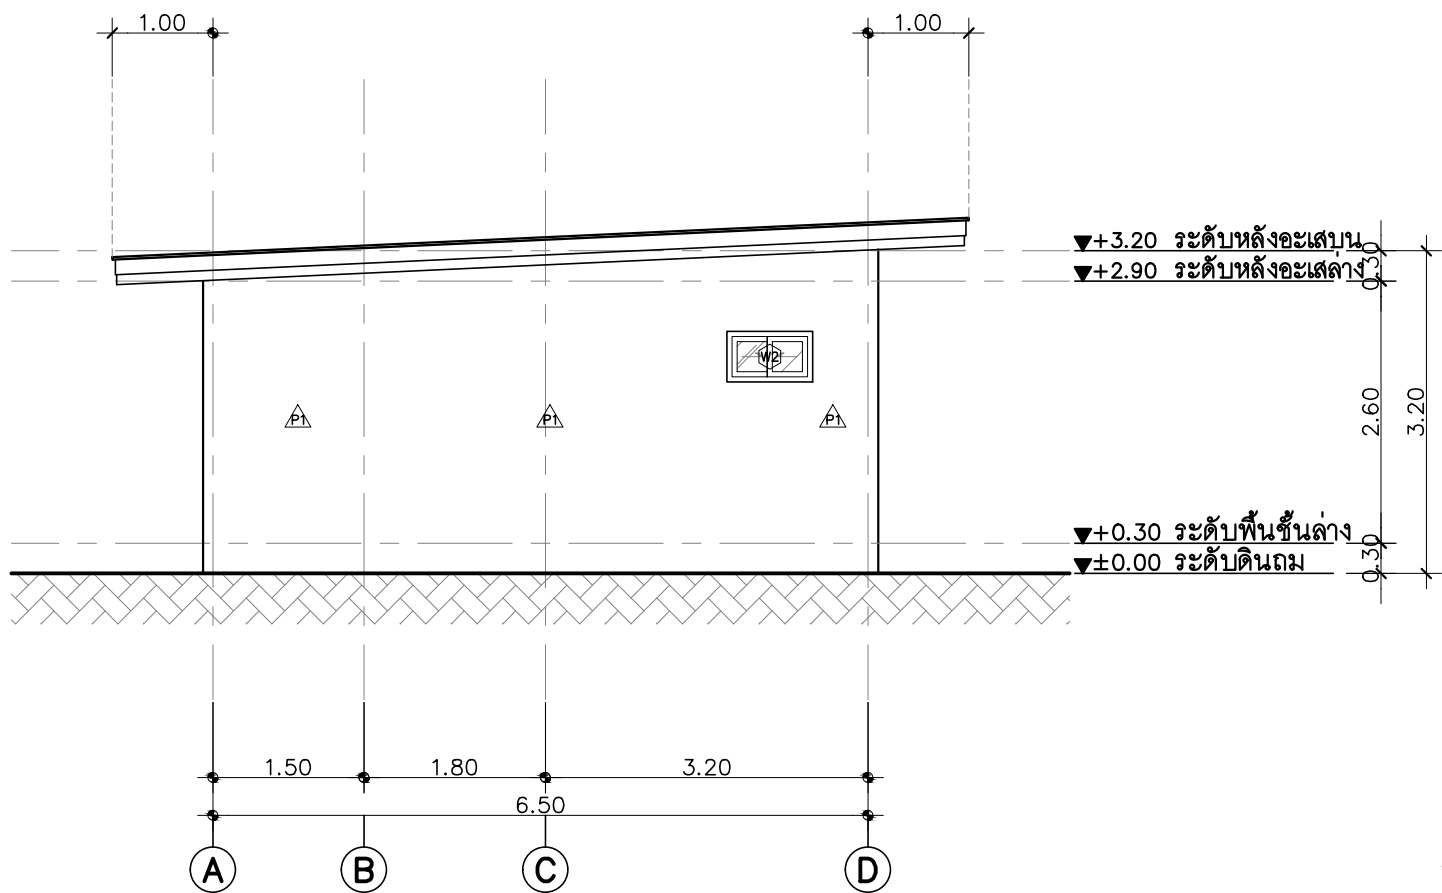


รูปด้าน 4
มาตราส่วน 1: 75

PROJECT NAME	
สำนักงานนิติบุคคลหมู่บ้านจัดสรร ทฤษฎา 33	
LOCATION	
ตำบลบางแม่นาง	
อำเภอบางใหญ่ จังหวัดนนทบุรี	
OWNER	
นิติบุคคลหมู่บ้านจัดสรรทฤษฎา33	
ARCHITECTS	
-	
-	
-	
ENGINEERS	
TITLE	
รูปด้าน 3	
รูปด้าน 4	
REVISION	
1	2
3	4
5	6
7	
DRAWN BY	
-	
DATE	2025-09-01
DRAWING NO.	TOTAL
A-06	OF

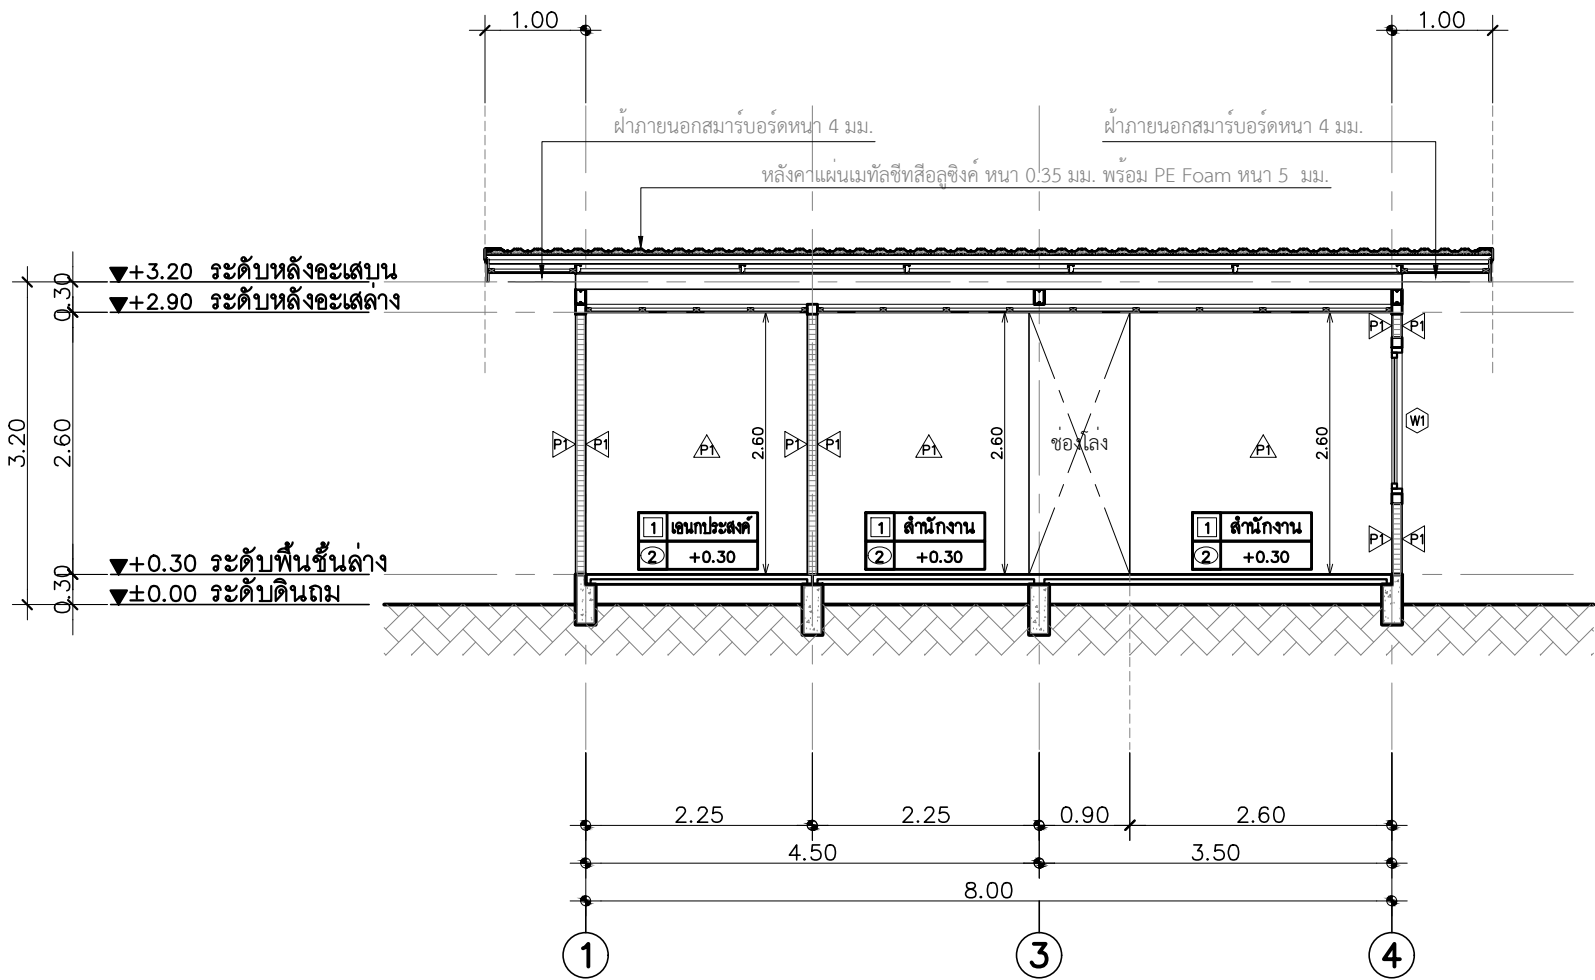


รูปตัด A
มาตราส่วน 1:75

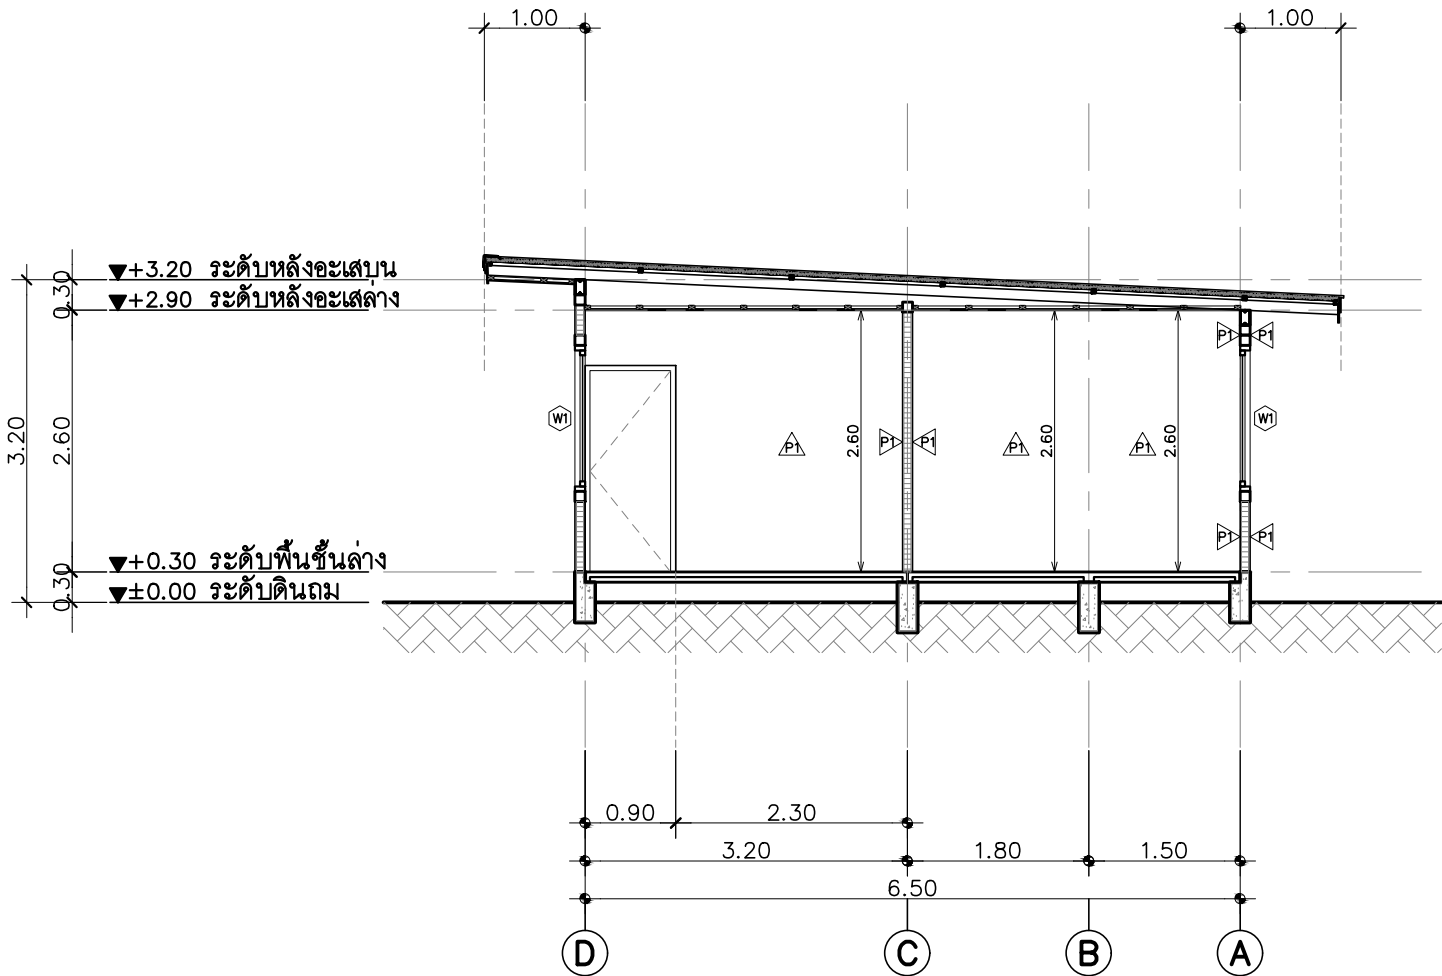


รูปตัด B
มาตราส่วน 1:75


PROJECT NAME						
สำนักงานนิติบุคคลหมู่บ้านจัดสรร พฤษภา 33						
LOCATION						
ตำบลบางแม่นาง						
อำเภอบางใหญ่ จังหวัดนนทบุรี						
OWNER						
นิติบุคคลหมู่บ้านจัดสรรพฤษภา33						
ARCHITECTS						
-						
-						
-						
ENGINEERS						
TITLE						
รูปตัด A						
-						
REVISION						
1	2	3	4	5	6	7
DRAWN BY						
-						
.						
DATE	2025-09-01					
DRAWING NO.	TOTAL					
A-07	OF					

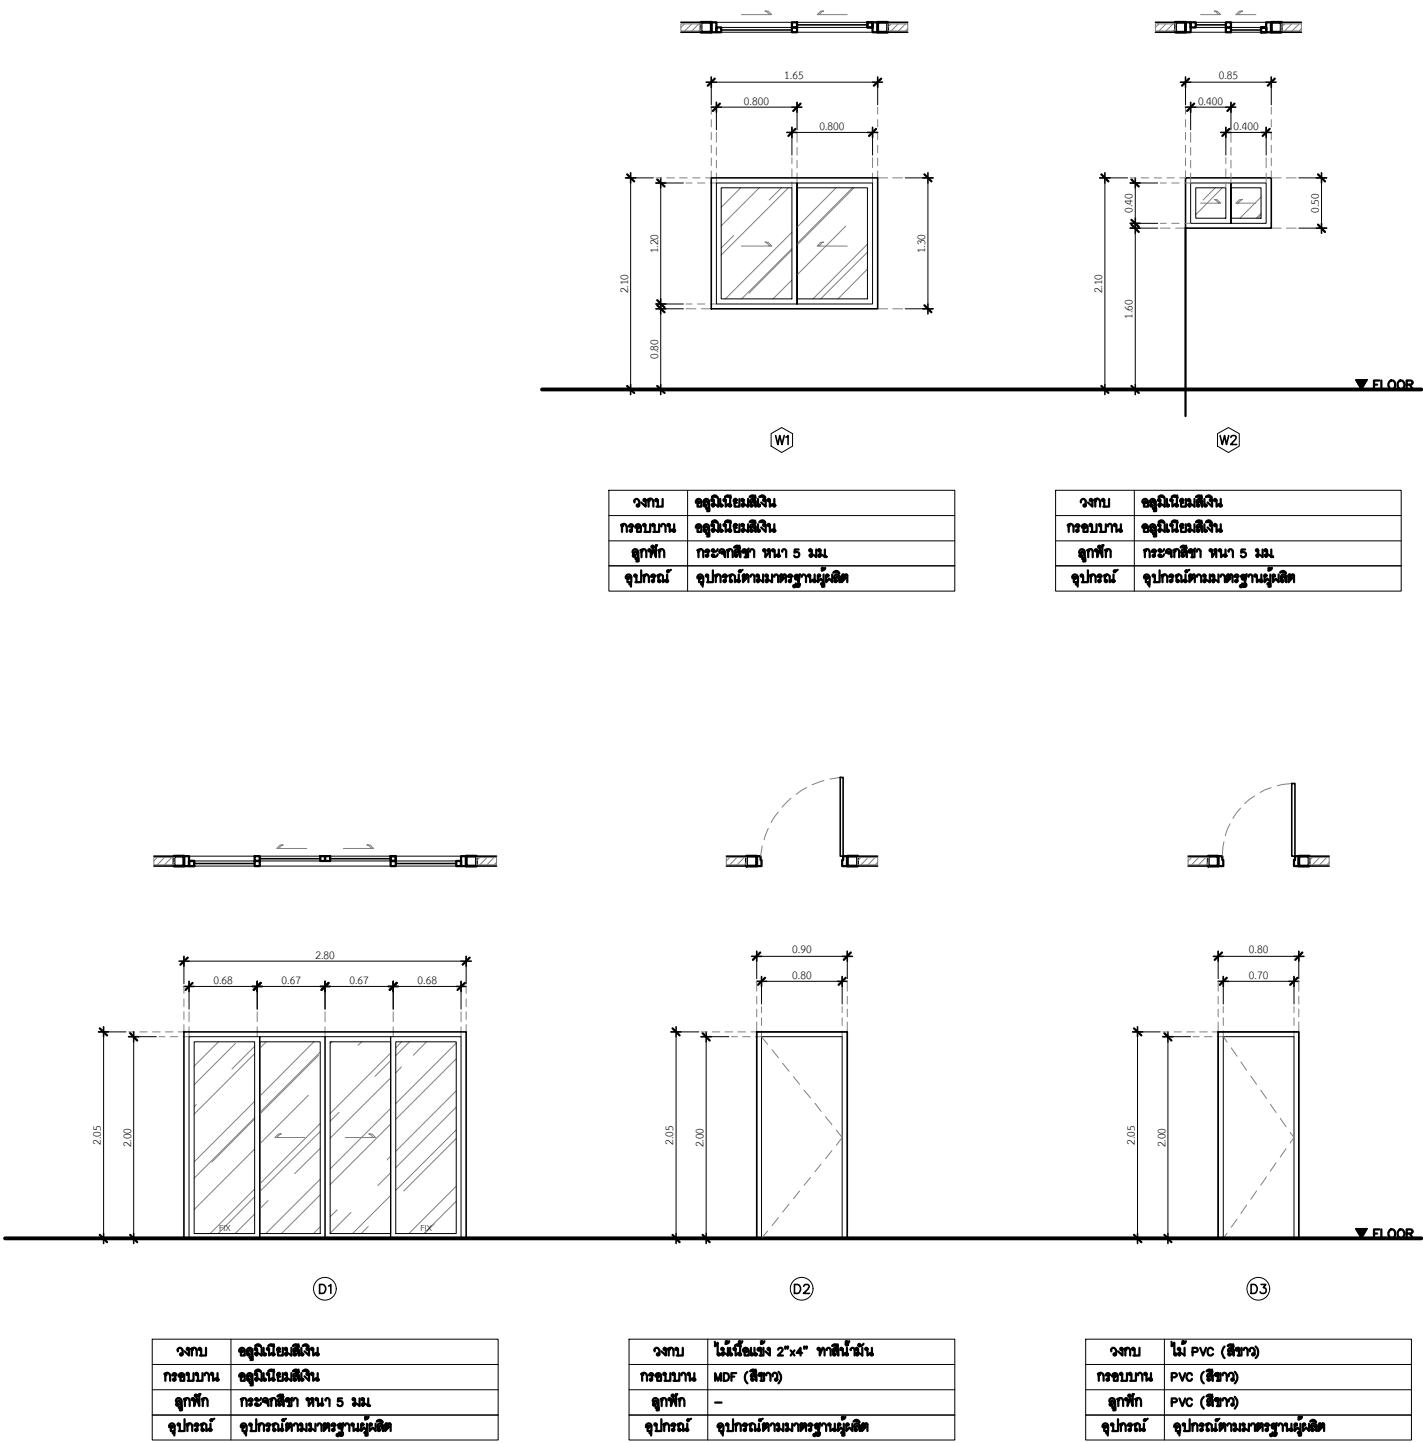


PROJECT NAME						
สำนักงานนิติบุคคลหมู่บ้านจัดสรร พฤษภา 33						
LOCATION						
ตำบลบางแม่นาง						
อำเภอบางใหญ่ จังหวัดนนทบุรี						
OWNER						
นิติบุคคลหมู่บ้านจัดสรรพฤษภา33						
ARCHITECTS						
-						
-						
-						
ENGINEERS						
TITLE						
แบบขยายประตู						
แบบขยายหน้าต่าง						
REVISION						
1	2	3	4	5	6	7
DRAWN BY						
-						
.						
DATE		2025-09-01				
DRAWING NO.		TOTAL				
A-08		OF				

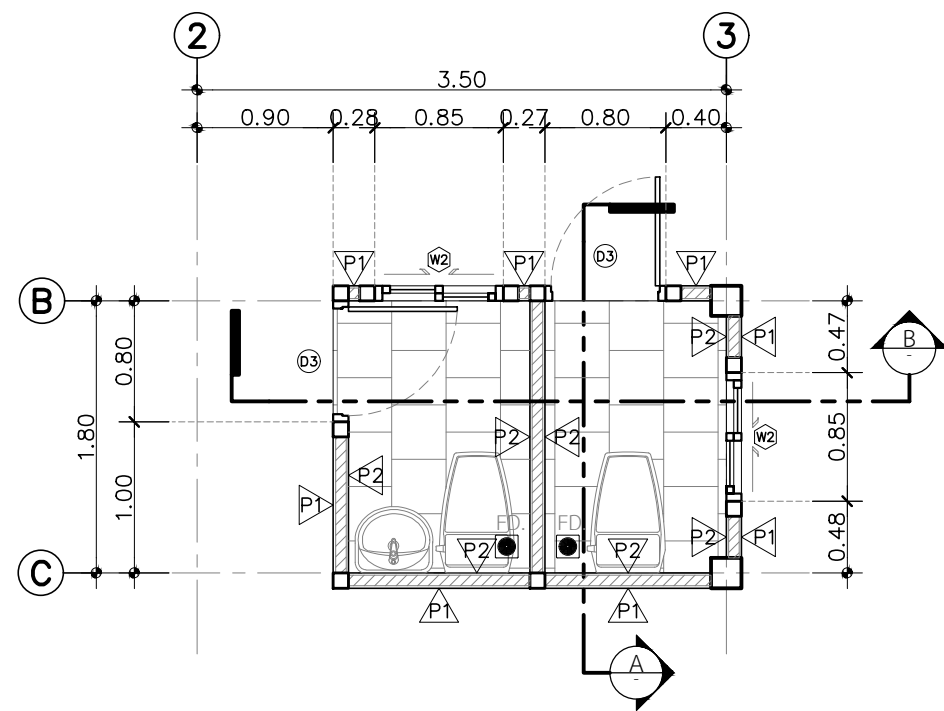

แปลน ห้องน้ำ WC1, WC2
มาตราส่วน 1:50

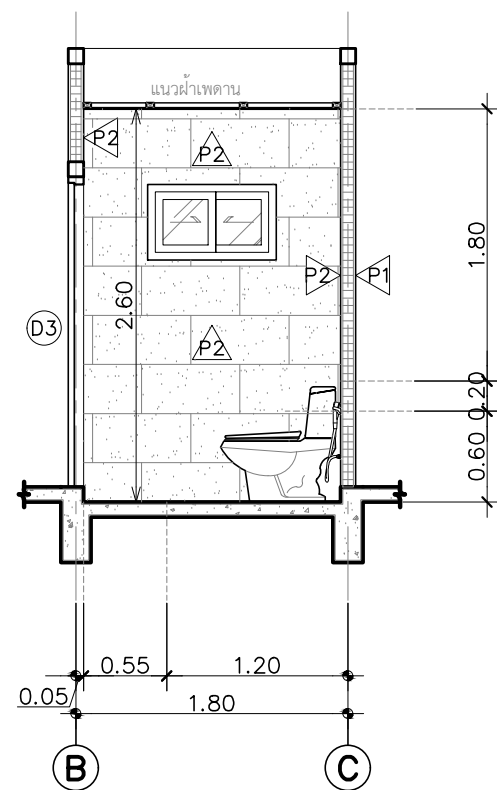

รูปตัด A (ห้องน้ำ WC2)
มาตราส่วน 1:50

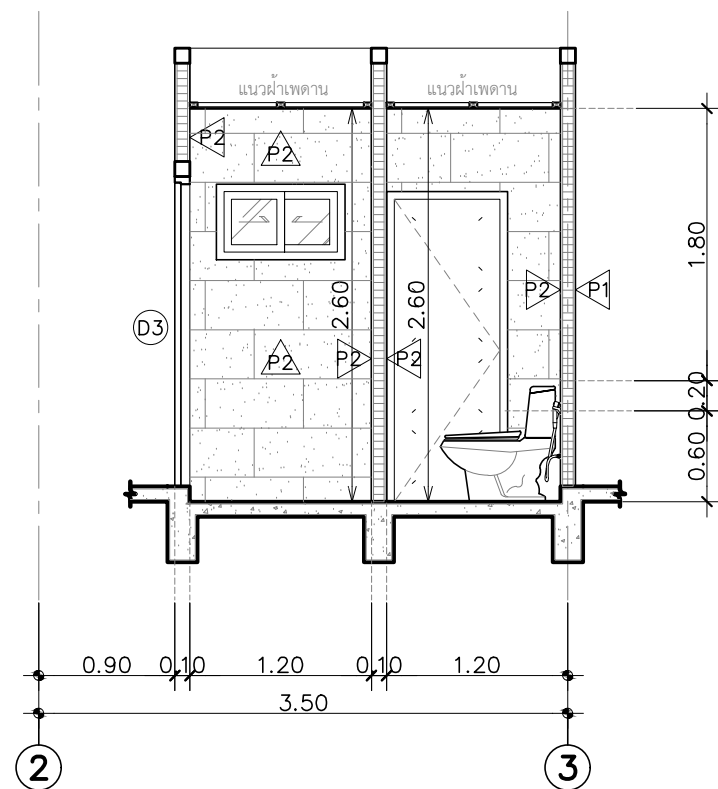

รูปตัด B (ห้องน้ำ WC1, WC2)
มาตราส่วน 1:50

PROJECT NAME						
สำนักงานนิติบุคคลหมู่บ้านจัดสรร พฤษา 33						
LOCATION						
ตำบลบางแม่นาง						
อำเภอบางใหญ่ จังหวัดนนทบุรี						
OWNER						
นิติบุคคลหมู่บ้านจัดสรรพฤษา33						
ARCHITECTS						
-						
-						
-						
ENGINEERS						
-						
-						
-						
TITLE						
แบบขยายห้องน้ำ						
-						
REVISION						
1	2	3	4	5	6	7
DRAWN BY						
-						
.						
DATE	2025-09-01					
DRAWING NO.	TOTAL					
A-09	OF					

[illegible]

PROJECT NAME						
สำนักงานนิติบุคคลหมู่บ้านจัดสรร พฤษภา 33						
LOCATION						
ตำบลบางแม่นาง						
อำเภอบางใหญ่ จังหวัดนนทบุรี						
OWNER						
นิติบุคคลหมู่บ้านจัดสรรพฤษภา33						
ARCHITECTS						
-						
-						
-						
ENGINEERS						
TITLE						
สารบัญและรายการประกอบแบบ						
REVISION						
1	2	3	4	5	6	7
DRAWN BY						
DATE	2025-09-01					
DRAWING NO.	TOTAL					
S-01	OF					

ความหมายและคำย่อ

fy = กำลังคดากของเหล็กเสริม

fc' = กำลังอัดประลัยของคอนกรีต

D = เส้นผ่าศูนย์กลางระบุของเหล็กเสริม

1/4 Stir = เหล็กปลอก, เหล็กผูกตั้ง

๑ = ระยะห่างจากศูนย์กลาง ถึงศูนย์กลาง

± = ไม่มากกว่า, ไม่เกิน

± = ไม่น้อยกว่า

DOUBLE = คู่ หมายถึง เหล็กปลอก 2 ปลอกขนาดเดียวกันวางชิดกัน

(4 LEGS) = 4 ขา หมายถึงเหล็กปลอก 2 ปลอก ปลอกเล็ก 1 ปลอก, ปลอกใหญ่ 1 ปลอก วางชิดกัน

T&B = บนและล่าง (TOP AND BOTTOM)

F&R = หน้าและหลัง (FRONT AND REAR)

B?(x?) = ตัวเลขในวงเล็บ เลขตัวหน้าหมายถึงความกว้าง เลขตัวหลังหมายถึงความลึก

S?(?), W?(?) = ตัวเลขในวงเล็บหลังชื่อพื้น, ผนัง หมายถึง ความหนาของพื้น, ผนัง

B1/B2 = คาน 2 ระดับโดยที่คาน B1 อยู่ระดับบน B2 อยู่ระดับล่าง

E = ระยะทาง, ระยะฝั่งของเหล็กเสริม

การแบ่งประเภทคอนกรีต และเกณฑ์กำหนดเกี่ยวกับการกำลังอัด

ชนิดของการก่อสร้าง	ค่าต่ำสุดของกำลังอัด ของแท่งกระบอกคอนกรีต หลังเทแล้ว 28 วัน เมกกาปาสกาล (กก/ซม๒)
- เสาเข็ม	24 MPa (240 ksc.)
- ฐานราก	24 MPa (240 ksc.)
- เสา	24 MPa (240 ksc.)
- พื้น	24 MPa (240 ksc.)
- คาน, คานขอยผนังคอนกรีตเสริมเหล็กที่ ใ้รับน้ำหนักหนาตั้งแต่ 100 มม ขึ้นไป แผ่นพื้นและดั่งกับน้ำ	24 MPa (240 ksc.)
- ผนังคอนกรีตเสริมเหล็กที่บางกว่า 100มม ที่ไม่ได้รับน้ำหนัก และครีบ คสล	24 MPa (240 ksc.)
- บันได และอื่นๆ	24 MPa (240 ksc.)
- คอนกรีตหยาบ 1:3:5	-

คุณสมบัติของเหล็กเสริม

- เหล็กเส้นกลมธรรมดา ให้ใช้เหล็กที่มีมาตรฐานตาม SR 24 ของมาตรฐานผลิตภัณฑ์อุตสาหกรรม มอก. 20–2543 โดยมีจุดคดากไม่น้อยกว่า 24 เมกกาปาสกาล
- เหล็กข้ออ้อยให้ใช้เหล็กที่มีมาตรฐานตาม SD 40 ของมาตรฐานผลิตภัณฑ์อุตสาหกรรมโดยมีจุดคดากไม่น้อยกว่า 40 เมกกาปาสกาล หรือใช้เหล็กที่มีมาตรฐานตาม SD 50 ของมาตรฐานผลิตภัณฑ์อุตสาหกรรม มอก. 24–2548 โดยมีจุดคดากไม่น้อยกว่า 50 เมกกาปาสกาล โดยพิจารณาใช้เหล็กเสริมคอนกรีตแต่ละคุณภาพตามแต่ลักษณะโครงสร้าง ดังนี้

ลักษณะโครงสร้าง	คุณภาพเหล็กเสริม
เสาเข็ม	SD 40
ฐานราก, เสา	SD 40
ผนัง คสล. (SHEAR WALL)	SD 40
พื้น, คาน	SD 40
บันได, ขึ้นๆ	SD 40

รอยต่อในเหล็กเสริม

ชนิดของอาคาร	ชนิดของรอยต่อ	ตำแหน่งของรอยต่อ
คาน, แผ่นพื้น	ต่อทาบ, ต่อเชื่อม (สำหรับเหล็กเส้น ขนาดเส้นผ่าศูนย์กลางมากกว่า 32 มิลลิเมตร)	ตามที่ได้รับอนุมัติ สำหรับคาน เหล็กบนให้ต่อที่บริเวณกลางคาน เหล็กล่างต่อที่หน้าเสา ถึงระยะ L/5 จากศูนย์กลางเสา
เสา, ผนัง	ต่อทาบ หรือต่อเชื่อม	เหนือระดับพื้น 1 เมตร จนถึงระดับ 1 เมตร ได้พื้นขึ้นบน
ฐานราก	สำหรับด้านที่สั้นกว่า ความยาวของเหล็ก มาตรฐาน ห้ามต่อ	

ระยะทาง, ระยะฝั่งสำหรับเหล็กเสริมในคาน, เสา, ผนังหนาตั้งแต่ 200 มม ขึ้นไป และฐานราก

ชนิดของเหล็กเสริม	เส้นผ่าศูนย์กลางของเหล็กเสริม (มม.)	ระยะทาง, ระยะฝั่งของเหล็กเสริม (มม.)	
		เหล็กเสริมบน (TOP BAES)	เหล็กเสริมอื่นๆ (OTHER BAES)
เหล็กข้ออ้อย (DEFORMED BARS) SD 40	12	500	400
	16	650	500
	20	800	650
	25	1,250	950
	28	1,400	1,100
	32	2,150	1,650
เหล็กข้ออ้อย (DEFORMED BARS) SD 50	10	500	400
	12	600	500
	16	800	650
	20	1,000	800
	25	1,550	1,200
	28	1,750	1,350
เหล็กผิวเรียบ (PLAIN BARS)	6	250	250
	9	400	400

ระยะทาง, ระยะฝั่งของเหล็กเสริมในผนัง, หนาไม่เกิน 200 มม และพื้น

ชนิดของเหล็กเสริม	เส้นผ่าศูนย์กลางของเหล็กเสริม (มม.)	ระยะทาง, ระยะฝั่งของเหล็กเสริม (มม.)	
		เหล็กเสริมบน (TOP BAES)	เหล็กเสริมอื่นๆ (OTHER BAES)
เหล็กข้ออ้อย (DEFORMED BARS) SD 40	12	450	350
	16	700	550
	20	1,000	800
	25	1,600	1,250
	28	1,950	1,500
เหล็กข้ออ้อย (DEFORMED BARS) SD 50	10	500	400
	12	600	500
	16	900	700
	20	1,300	1,000
	25	2,000	1,500
	28	2,400	1,850
เหล็กผิวเรียบ (PLAIN BARS)	6	250	250
	9	400	400


หมายเหตุ

- เหล็กเสริมบน หมายถึง เหล็กเสริมตามแนวนอน ที่มีความหนาของคอนกรีต ใต้ระดับเหล็กเสริมนั้น มากกว่า 300 มม
- สำหรับการทาบเหล็กล่าง กลางช่วงขององค์อาคาร ได้แก่ พื้น หรือคานพับ ให้เพิ่มระยะทาบเป็น 1.3 เท่า ของค่าที่แสดงในตาราง


PROJECT NAME						
สำนักงานนิติบุคคลหมู่บ้านจัดสรร ทฤศฯ 33						
LOCATION						
ตำบลบางแม่นาง						
อำเภอบางใหญ่ จังหวัดนนทบุรี						
OWNER						
นิติบุคคลหมู่บ้านจัดสรรทฤศฯ33						
ARCHITECTS						
-						
-						
-						
ENGINEERS						
TITLE						
รายละเอียดและข้อกำหนดทั่วไป 2						
REVISION						
1	2	3	4	5	6	7
DRAWN BY						
DATE	2025-09-01					
DRAWING NO.	TOTAL					
S-03	OF					

รายละเอียดและข้อกำหนดเกี่ยวกับการเสริมเหล็กเสา


① ในกรณีที่เสาขนาดตั้งอยู่บนเสาขนาดใหญ่กว่าให้เสริมเหล็กดังรูป

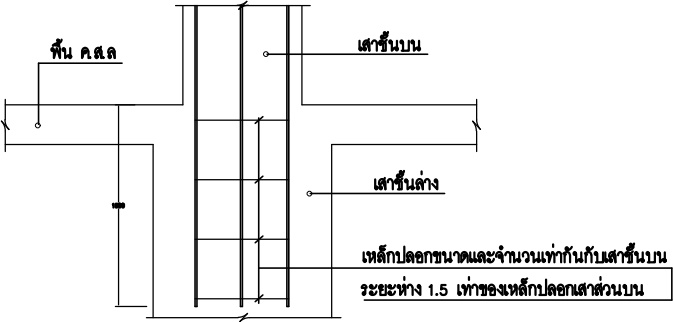


② การเสริมเหล็กเสาที่ตั้งบนคาน

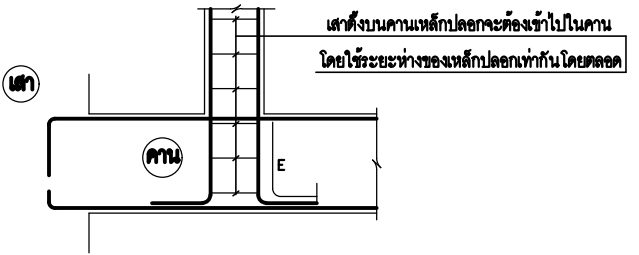


③ การเสริมเหล็กเสาที่ตั้งบนฐานราก

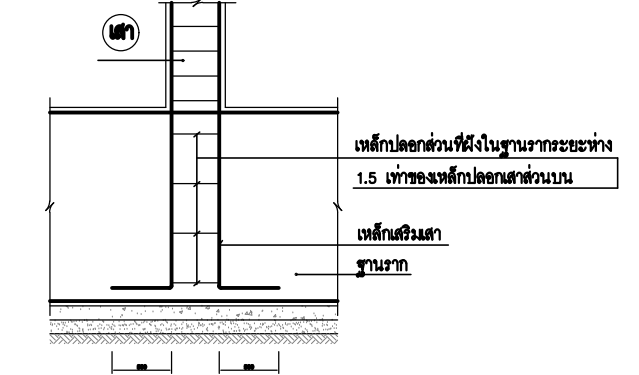

④ การเสริมเหล็กปลอกบริเวณจุดต่อ

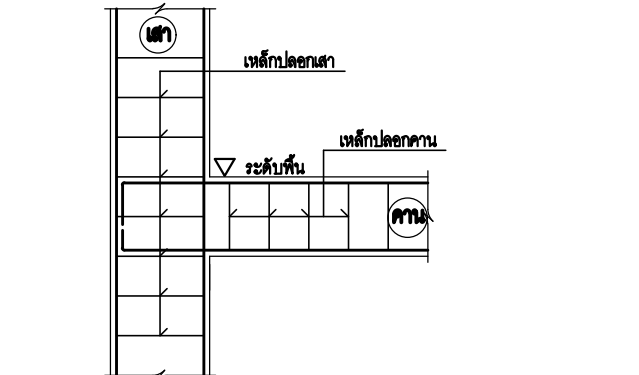


⑤ การต่อเหล็กเสา (กรณีพบเหล็ก)

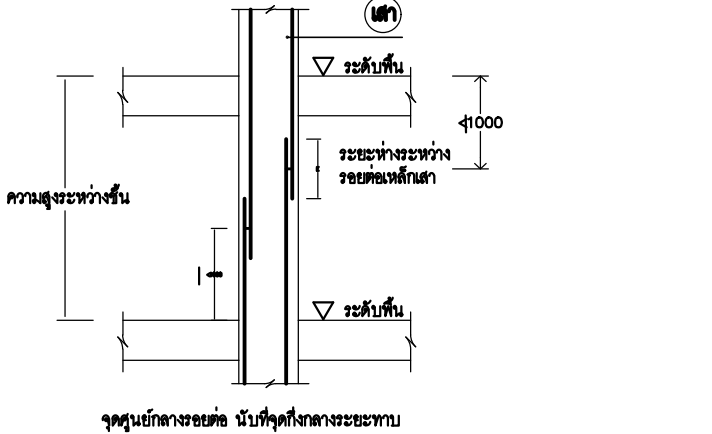


⑥ เสาประกอบด้วยเหล็กรูปพรรณ

- กรณีที่เหล็กรูปพรรณขวางเหล็กปลอก ให้เชื่อมเหล็กปลอกเข้ากับเหล็กรูปพรรณ
- เหล็กแกนคาน FRAME หรือคานต่อเนื่องจะต้องถ่ายแรงด้วย TRANSFERED STEEL PLATE

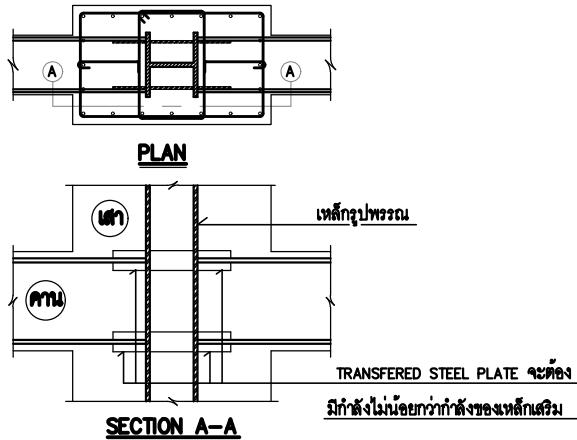

⑦ บริเวณรอยต่อระหว่างเสากับคานหรือพื้นจะต้องเสริมเหล็กปลอกของเสา ต่อเนื่องตลอด และต้องเพิ่มเหล็กปลอกของเสาด้วยจำนวนและขนาดของเหล็กปลอกเท่าเดิม เพื่อให้ระยะห่างของเหล็กปลอก (SPACINGS) ลดลงครึ่งหนึ่ง ในบริเวณทั้งเหนือและใต้รอยต่อ เป็นระยะไม่น้อยกว่า 1 ใน 3 (1/3) ของความสูงใต้ระดับพื้นหรือคานชั้นล่าง ถึงระดับด้านบนของพื้นชั้นบน ในแต่ละช่วงชั้น (h) โดยจะต้องไม่น้อยกว่า 1000 มม. ดูตัวอย่างตามรูป

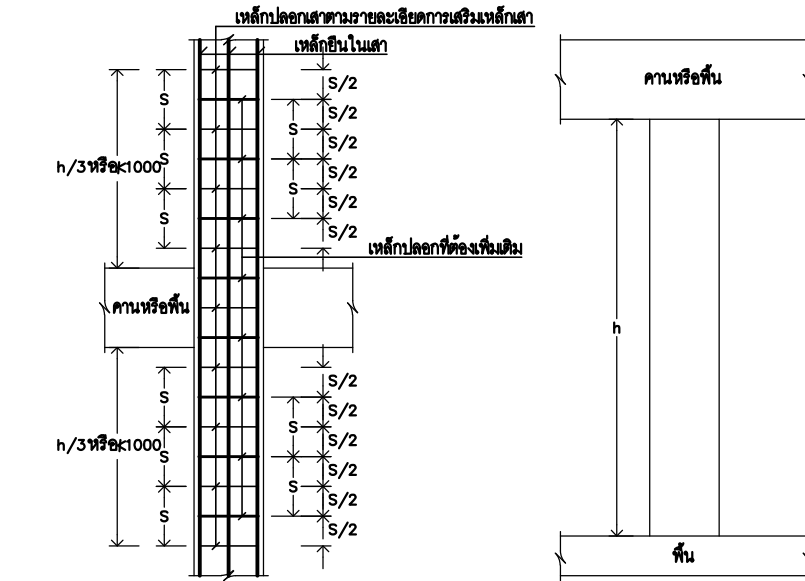


ลักษณะการเสริมเหล็กปลอกบริเวณรอยต่อระหว่างเสาและคานหรือพื้น


รายละเอียดและข้อกำหนดเกี่ยวกับการเสริมเหล็กคาน

① เหล็กปลอกเสริมพิเศษในคาน ค.ส.ล


สำหรับคาน ค.ส.ล ที่หนาตั้งแต่ 200 มม ขึ้นไป ที่ทุกหนึ่งในสามของชั้นจะต้องเสริมเหล็กปลอก แต่ระยะห่างต้องไม่เกิน 1000 มม (ถ้าหนาน้อยกว่า 200 มม ให้ยึดห่างไม่เกิน 1500 มม)

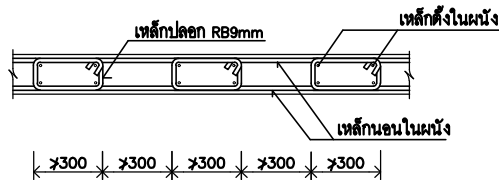

② การเสริมเหล็กบริเวณมุม หรือ รอยต่อของคาน

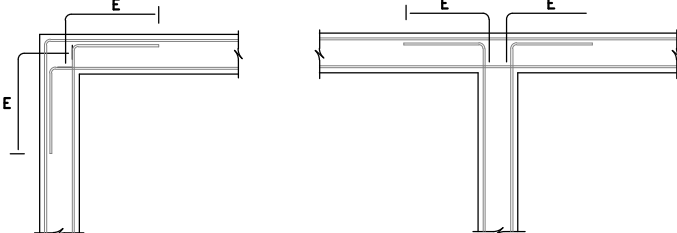


③ การเสริมเหล็กคานทั่วไปที่ไม่ได้ระบุ

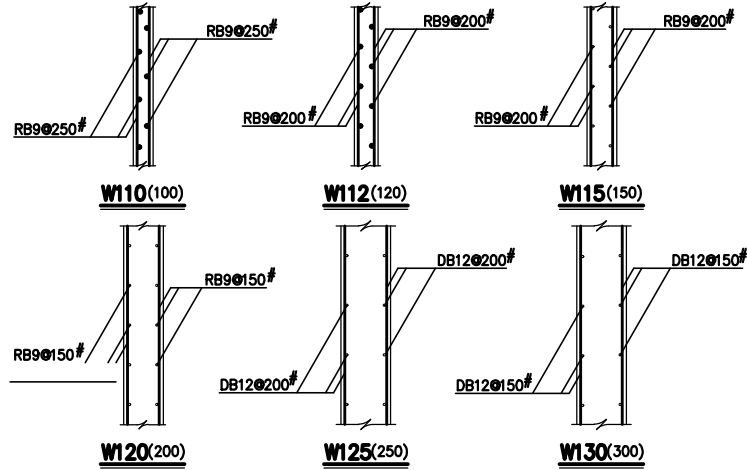

- คาน ค.ส.ล ทุกคานที่ไม่มีคานรองรับที่ส่วนบนสุด และล่างสุดของคานให้เสริมเหล็กพิเศษที่ปลายบนสุด และล่างสุด ในกรณีที่ไม่ได้ระบุดังต่อไปนี้

- คานหนา 100mm เสริมเหล็ก 2DB12
- คานหนา 120mm เสริมเหล็ก 4DB12
- คานหนา 150mm เสริมเหล็ก 4DB16
- คานหนา 200mm เสริมเหล็ก 4DB20
- คานหนา 250mm เสริมเหล็ก 4DB25
- คานหนา 300mm เสริมเหล็ก 4DB25

④ การเสริมเหล็กพิเศษในคาน ตามข้อ ③

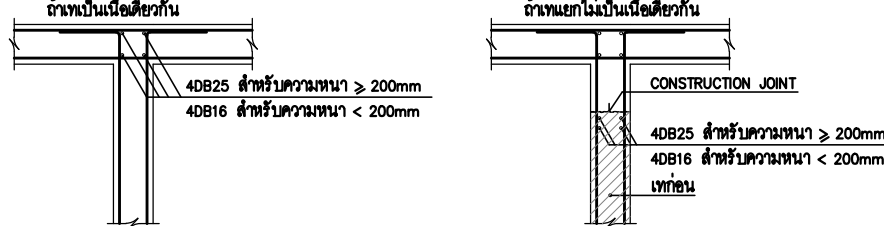


⑤ ส่วนคานและคาน ค.ส.ล ต่าง ๆ ตามแบบสถาปัตยกรรมที่ได้ระบุในแบบโครงสร้าง

ให้ใช้รายละเอียดการเสริมเหล็ก W110, W112, W115, W120, W125, W130


ตามความหนาที่สอดคล้องตามแบบสถาปัตยกรรม

⑥ ในกรณีที่มีการเจาะช่องเปิดในคาน ค.ส.ล ที่ขนาดไม่เกิน 1000x1000mm ให้เหล็กเสริมพิเศษอย่างน้อย ดังรูปข้างล่าง

โดยที่ความแข็งแรงของคาน ค.ส.ล ที่เจาะช่องเปิด จะต้องไม่น้อยกว่าความแข็งแรงของคาน ค.ส.ล เดิม

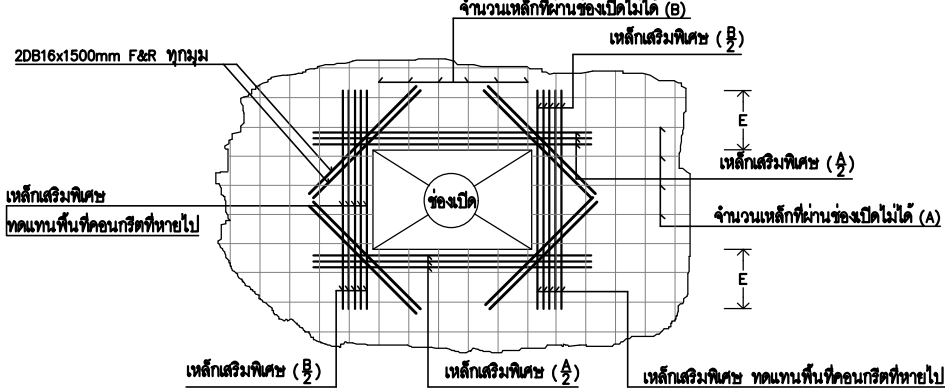

รายละเอียดการเสริมเหล็กในคานค้ำ และคานห้อย ในกรณีที่ไม่ได้ระบุในแบบ

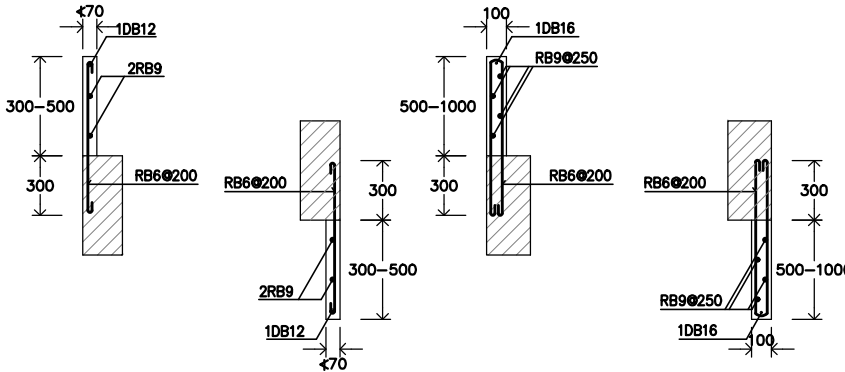


PROJECT NAME						
สำนักงานนิติบุคคลหมู่บ้านจัดสรร พฤษภา 33						
LOCATION						
ตำบลบางแม่นาง						
อำเภอบางใหญ่ จังหวัดนนทบุรี						
OWNER						
นิติบุคคลหมู่บ้านจัดสรรพฤษภา33						
ARCHITECTS						
-						
-						
-						
ENGINEERS						
-						
-						
-						
TITLE						
รายละเอียดและข้อกำหนดทั่วไป 3						
REVISION						
1	2	3	4	5	6	7
DRAWN BY						
DATE						
2025-09-01						
DRAWING NO.						
TOTAL						
S-04						
OF						


รายละเอียดและข้อกำหนดเกี่ยวกับการเสริมเหล็กคาน 1/2

1. การเสริมเหล็กคานบริเวณที่รองรับ (SUPPORT)


- 1.1 กรณีที่รองรับของคานเป็นเสา (COLUMN) หรือกำแพงคอนกรีตรับแรงเฉือน (SHEAR WALL) และไม่มีการเสริมเหล็กต่อเนื่องระหว่างคานทั้ง 2 ด้านของที่รองรับ เหล็กบนและเหล็กล่างจะต้องฝังที่รองรับ (SUPPORT) เป็นระยะ E

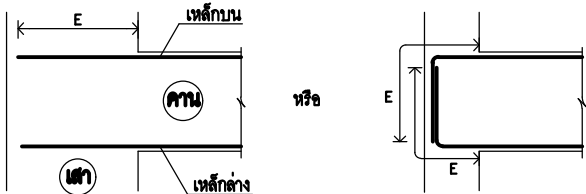

1.2 คานยื่น

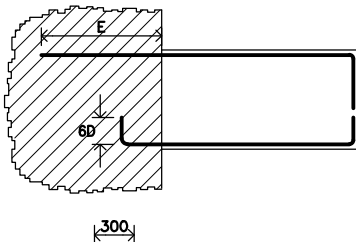


1.3 คานที่ไม่ได้มีระยะฝังเข้า SUPPORT (SIMPLY SUPPORT) และที่รองรับของคานเป็นคานด้วยกัน

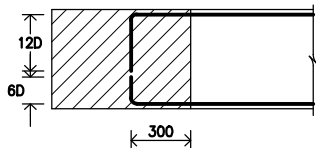


2. ในกรณีที่ต้องเทคอนกรีตคานเสาหรือผนังที่เทคอนกรีตเสร็จเรียบร้อยแล้ว ให้ปฏิบัติตามวิธีการต่อไปนี้

- ฝังเหล็กเสริมพิเศษลักษณะดังรูป
- เทบ่ารับคานโดยมีขนาดเท่ากับหน้าตัดคาน ความลึกเท่ากับ COVERING ของเสา

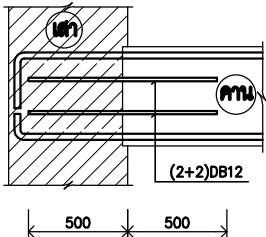


วิธีการนี้ใช้เฉพาะคานขนาดความลึก $\geq 600\text{mm}$ และความกว้าง $\geq 300\text{mm}$ ถ้าขนาดคานใหญ่กว่าที่กำหนดให้ทำรายการคำนวณเพื่อขออนุมัติ

3. การเสริมเหล็กคาน บริเวณหัก SLOPE

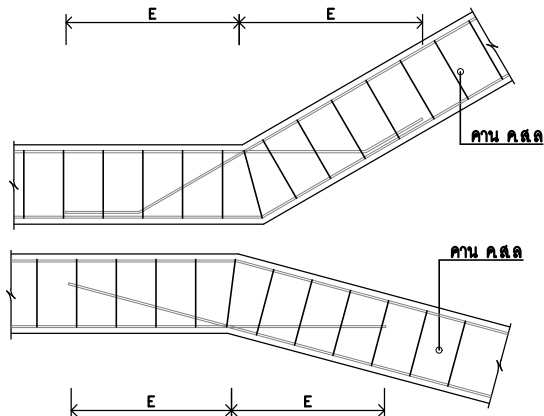


4. การฝัง SLEEVE ในคาน ค.ส.ล

สำหรับขนาดของ SLEEVE $\geq 150\text{mm}$ ให้ใช้รายละเอียดการเสริมเหล็กกรอบ SLEEVE ดังรูป

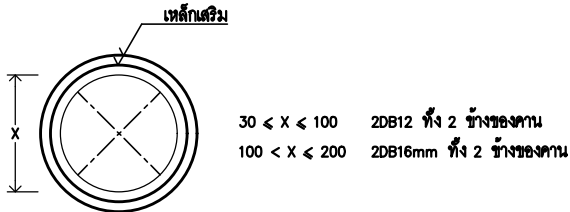

5. ข้อกำหนดสำหรับรายละเอียดการเสริมเหล็กปลอกพิเศษสำหรับคาน ในกรณีที่รองรับของคานเป็นเสา (COLUMN) หรือกำแพงคอนกรีตรับแรงเฉือน (SHEAR WALL)

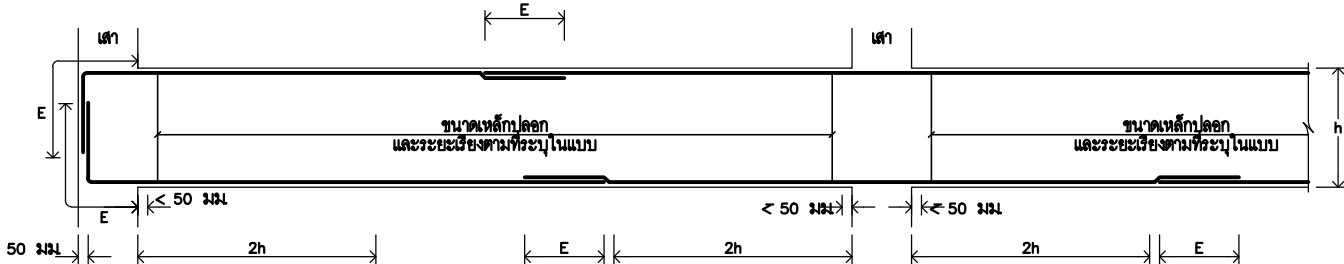

5.1 การทาบเหล็กตามยาวของคาน

- สำหรับเหล็กบนให้ทาบกลางช่วงคาน
- สำหรับเหล็กล่างห้ามให้ทาบกลางช่วงคาน ให้ทาบบริเวณใกล้ที่รองรับและจะต้องห่างจากขอบที่รองรับเป็น $2h$ โดย h คือ ความลึกของคาน

5.2 เหล็กปลอกลูกแรกจะต้องห่างจากขอบที่รองรับไม่เกิน 5 ซม


5.3 ระยะเรียงห่างสุดของเหล็กปลอกตามที่ระบุในแบบในบริเวณที่ล้อมรอบตลอดความยาวของการทาบเหล็กจะต้องไม่มากกว่า $h/4$ หรือ 10 ซม โดยใช้ค่าน้อยกว่าเป็นเกณฑ์

5.4 ระยะเรียงห่างสุดของเหล็กปลอกภายในระยะ $2h$ จากขอบที่รองรับจะต้องเป็นระยะที่น้อยที่สุดจากค่าดังต่อไปนี้

- $h/4$
- 8 เท่าของเส้นผ่านศูนย์กลางของเหล็กเสริมตามยาวที่เล็กที่สุด
- 24 เท่าของเส้นผ่านศูนย์กลางของเหล็กปลอก
- ไม่นเกิน 30 ซม

5.5 ในกรณีที่ระยะเรียงของเหล็กปลอกตามที่ระบุในแบบไม่สอดคล้องตามข้อ 5.4 และมีค่ามากกว่าหรือเท่ากับระยะเรียงมากที่สุดตามข้อ 5.4 ให้ปรับระยะเรียงของเหล็กปลอกให้สอดคล้องตามข้อ 5.4 ด้วยขนาดของเหล็กปลอกเดิมตามที่ระบุในแบบ

1. การเสริมเหล็กบนรับโมเมนต์ลบในพื้น ค.ส.ล

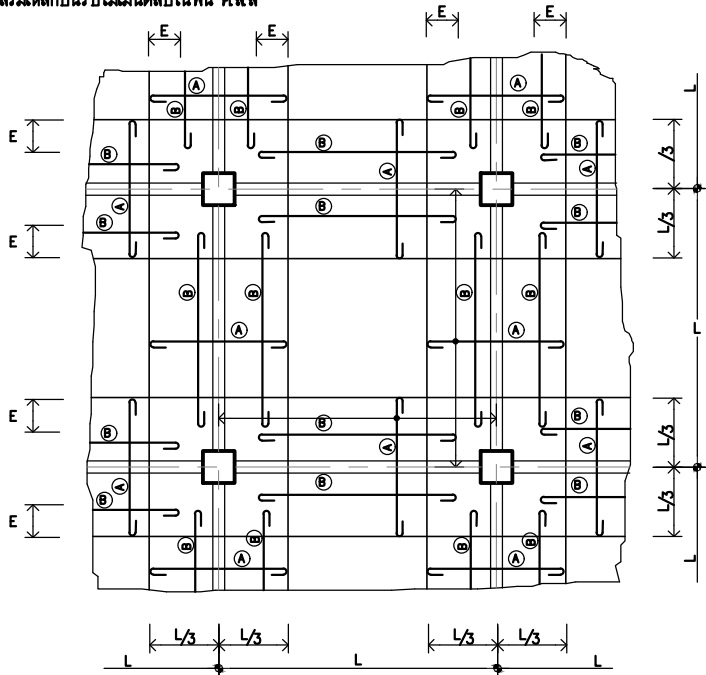


หมายเหตุ

- (A) = เหล็กเสริมบนรับโมเมนต์ลบ (NEGATIVE REINFORCEMENT) ของพื้น ค.ส.ล จะต้องเสริมตลอดแนวคาน
(B) = เหล็กเสริมที่ใช้สำหรับยึดเหล็กเสริมรับโมเมนต์ลบ (SPACER)


2. สำหรับแผ่นพื้นหุ้มดัดเหล็กบนที่บริเวณเหนือคาน และเหล็กล่างตรงกึ่งกลางท้องพื้น

3. การเรียงเหล็กในแผ่นพื้น ค.ส.ล ติดต่อกัน แต่คนละเบอร์ (หรือเบอร์เดียวกัน แต่ไม่ได้แสดงรูปตัดด้านนั้นในแบบ) ให้เดินเหล็กเหนือคานในบริเวณเท่ากับเหล็กท้องพื้น ของด้านที่มีเหล็กมากกว่า โดยเดินต่อเนื่องกันยาวด้านละ 1/3 ของช่วงยาว ดังตัวอย่างข้างล่าง ผู้รับเหมาจะต้องเสริมเหล็ก RB9@100 ตลอดช่วงคาน Bx

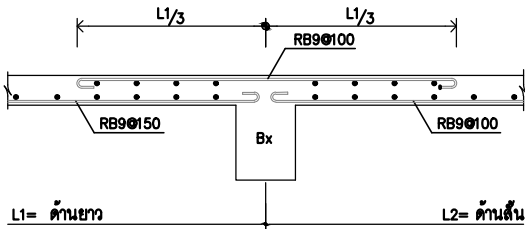


ในกรณีที่ยอดรับเป็นผนัง ค.ส.ล ให้เสริมเหล็กเชื่อมเดียวกับคาน

4. แผ่นพื้น ค.ส.ล ที่ไม่ต้องเนื่อง 2 ด้านบริเวณมุมของสองด้านนั้นให้เสริมเหล็กค้ำและเหล็กบนทแยงตามรูปเป็นระยะ 1/5 ของด้านยาวโดยขนาดและระยะห่างเท่ากับเหล็กค้ำกลางแผ่นพื้น ด้านที่มีบริเวณเหล็กมากกว่า

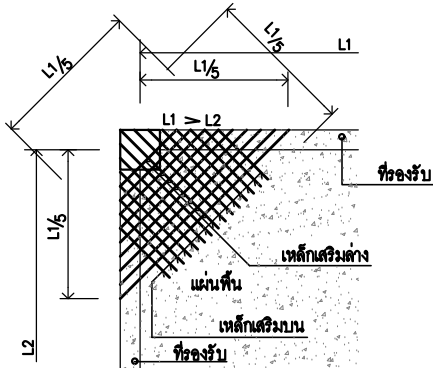


รายละเอียดและข้อกำหนดเกี่ยวกับการเสริมเหล็กในพื้นที่ทั่วไป


5. ทุกแห่งที่มีมุมแหลมมุมฉากที่ชนเข้าในแผ่นพื้น ค.ส.ล โดยไม่มีคานได้มุมแหลมหรือบริเวณพื้นที่ดักเป็นมุมให้เสริมเหล็กพิเศษขนาด 2RB9@40 ยาว 700mm ทั้งบนและล่างดังรูป

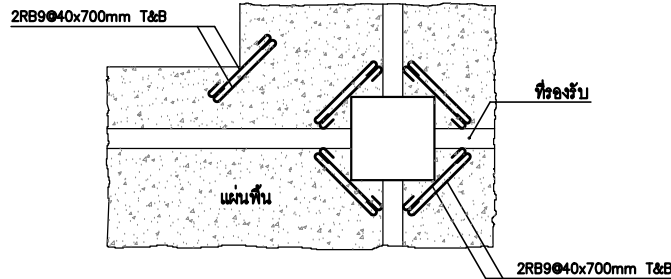


6. การเสริมเหล็กพื้น บริเวณหัก SLOPE

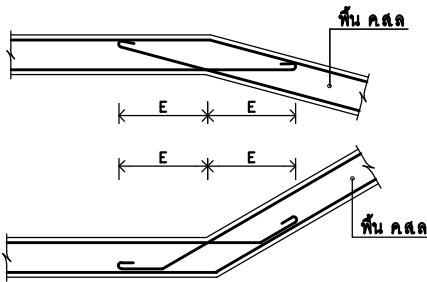


7. การเสริมระดับพื้นหนา 150

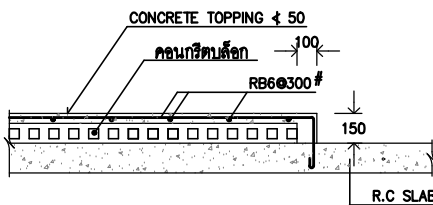

8. การเสริมระดับพื้นหนา 100

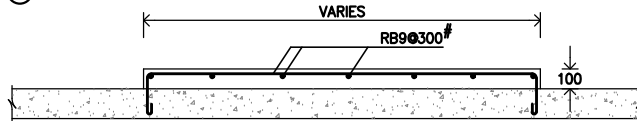


9. การเจาะช่องเปิดในแผ่นพื้น ค.ส.ล ให้เสริมเหล็กพิเศษอย่างน้อยเท่ากับพื้นที่หน้าตัด ของเหล็กที่ไม่สามารถผ่านช่องเปิดโดยกระจายไว้ 2 ข้างของช่องเปิดข้างละเท่าๆกัน และเสริมเหล็กพิเศษ 2DB12 ยาว 1000 mm ทั้งบนและล่างดังตัวอย่างข้างล่าง โดยที่ความแข็งแรงของแผ่นพื้น ค.ส.ล ที่เจาะช่องเปิดจะต้องไม่น้อยกว่าความแข็งแรงของพื้นเดิม ทั้งนี้จะต้องลงรายละเอียดการเสริมเหล็ก ตำแหน่งและขนาดของช่องเปิดให้วิศวกรผู้ออกแบบพิจารณาอนุมัติ

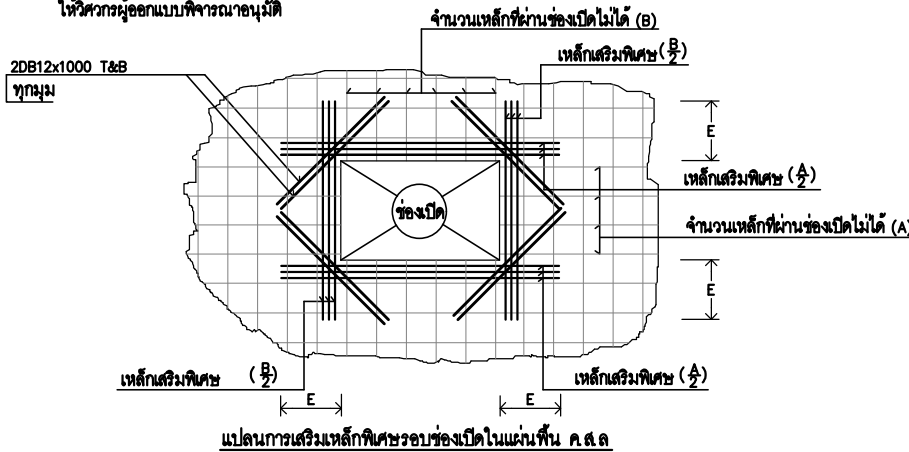


10. การฝัง SLEEVE ในแผ่นพื้น ค.ส.ล

สำหรับขนาดของ SLEEVE > 150 ให้ใช้รายละเอียดการเสริมเหล็กกรอบ SLEEVE ดังรูป
2RB9 T&B โดยที่เหล็ก RB9 ต้องเชื่อมปลายติดกันให้แข็งแรง

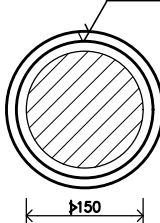


สำหรับขนาดของ SLEEVE > 150 ให้พิจารณาฝังเหล็กในพื้นที่ที่สามารถผ่านบริเวณ SLEEVE ได้โดยให้ใช้วิธีการเสริมเหล็กเหมือนข้อ 9
ทั้งนี้จะต้องลงรายละเอียดของการเสริมเหล็ก ตำแหน่ง และขนาดของช่องเปิดให้วิศวกรผู้ออกแบบพิจารณาอนุมัติ


รายละเอียดและข้อกำหนดเกี่ยวกับการเสริมเหล็กในพื้นที่เสาเข็ม

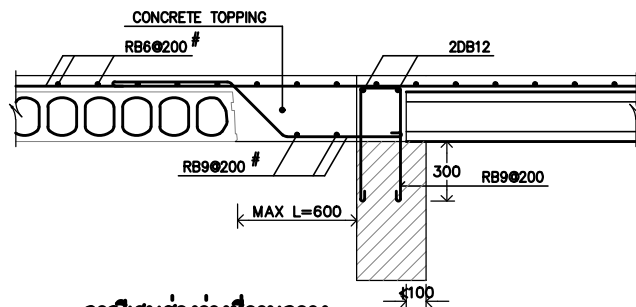


กรณีช่องว่างที่คานกลาง

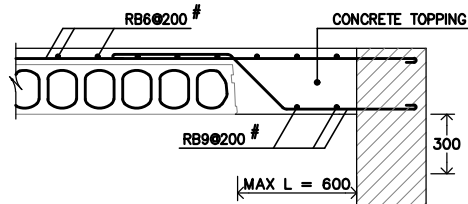


กรณีช่องว่างที่คานริม

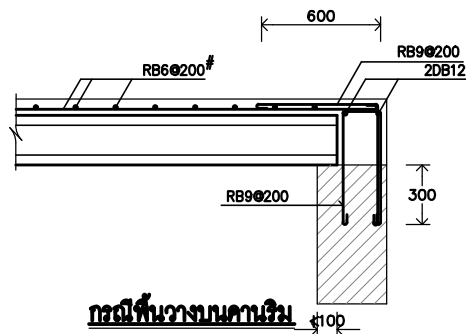


กรณีพื้นวางบนคานริม

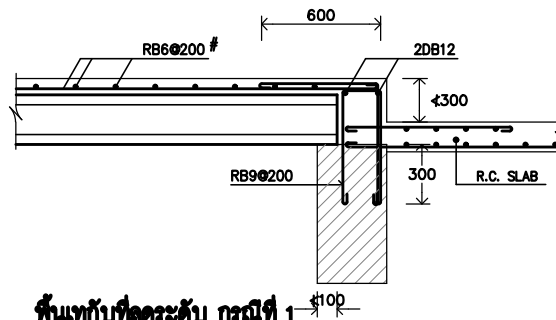

พื้นที่ทับซ้อนระดับ กรณีที่ 1

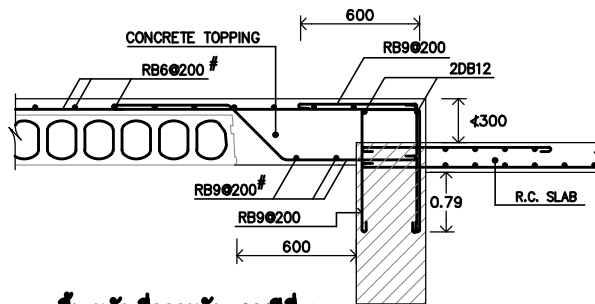


พื้นที่ทับซ้อนระดับ กรณีที่ 2

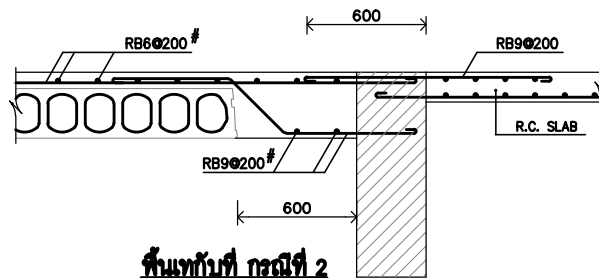

พื้นที่ทับซ้อน กรณีที่ 2


PROJECT NAME	
สำนักงานนิติบุคคลหมู่บ้านจัดสรร พฤษภา 33	
LOCATION	
ตำบลบางแม่นาง	
อำเภอบางใหญ่ จังหวัดนนทบุรี	
OWNER	
นิติบุคคลหมู่บ้านจัดสรรพฤษภา33	
ARCHITECTS	
-	
-	
-	
ENGINEERS	
-	
-	
-	
TITLE	
รายละเอียดและข้อกำหนดทั่วไป 5	
REVISION	
1	2
3	4
5	6
7	
DRAWN BY	
DATE	
2025-09-01	
DRAWING NO.	
TOTAL	
S-06	
OF	

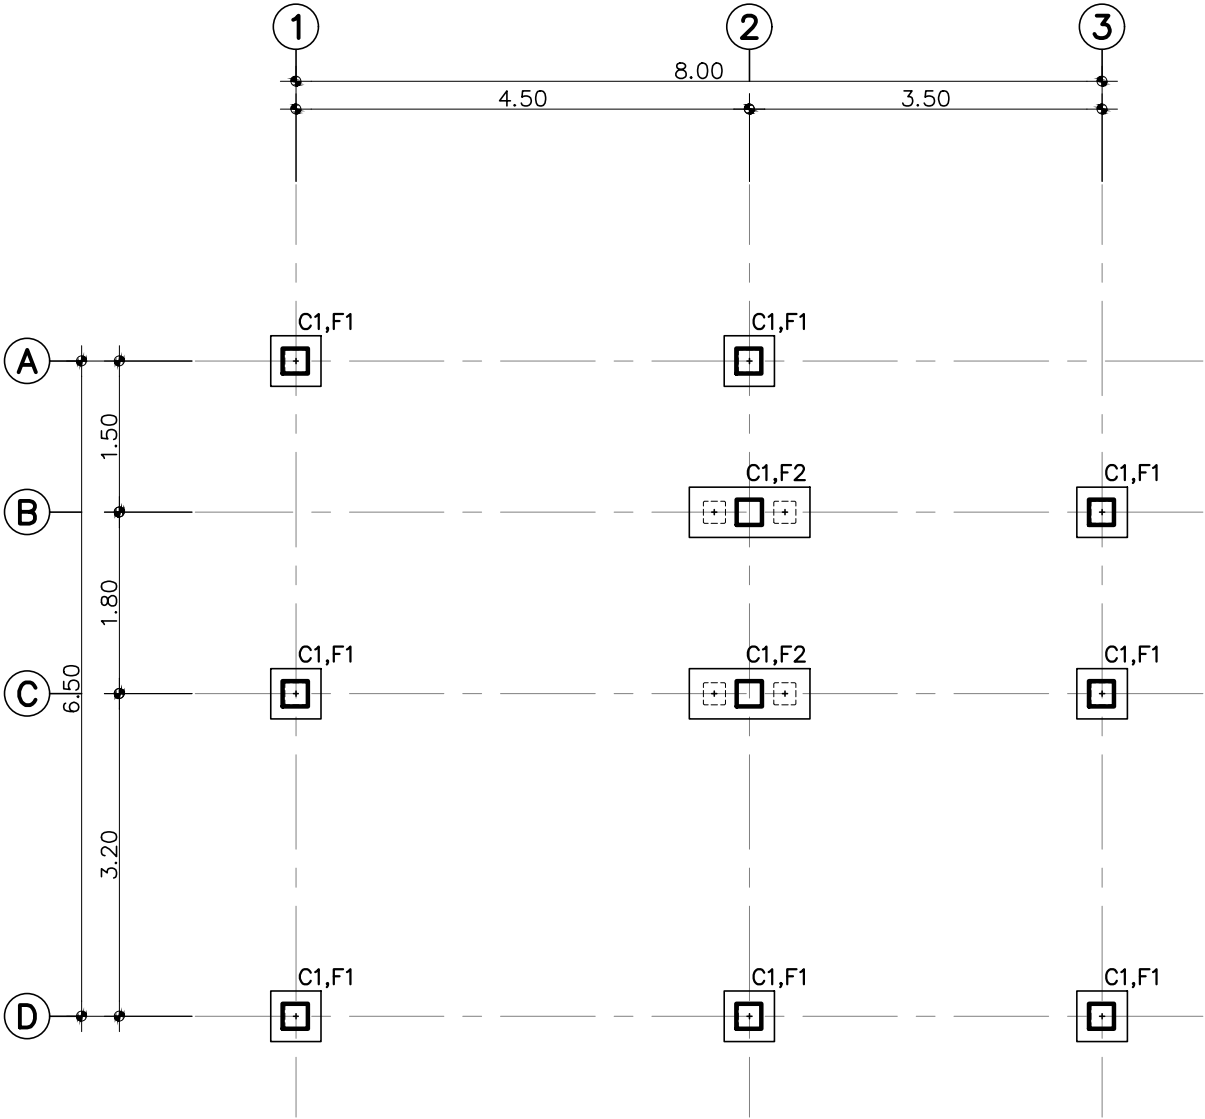

แปลนตำแหน่งฐานรากและเสาเข็ม

SCALE 1: 75

- หมายเหตุ
- ใช้เสาเข็มไมโครไพล์ขนาด 0.22X0.22X.....ม
รับน้ำหนักปลอดภัยได้ 25 เมตริกตัน/ต้น อัตราส่วนความ
ปลอดภัย (FS) เท่ากับ 2.5
 - ระยะและตำแหน่งของฐานราก-เสา ให้เป็นไปตามแบบสถาปัตยกรรม

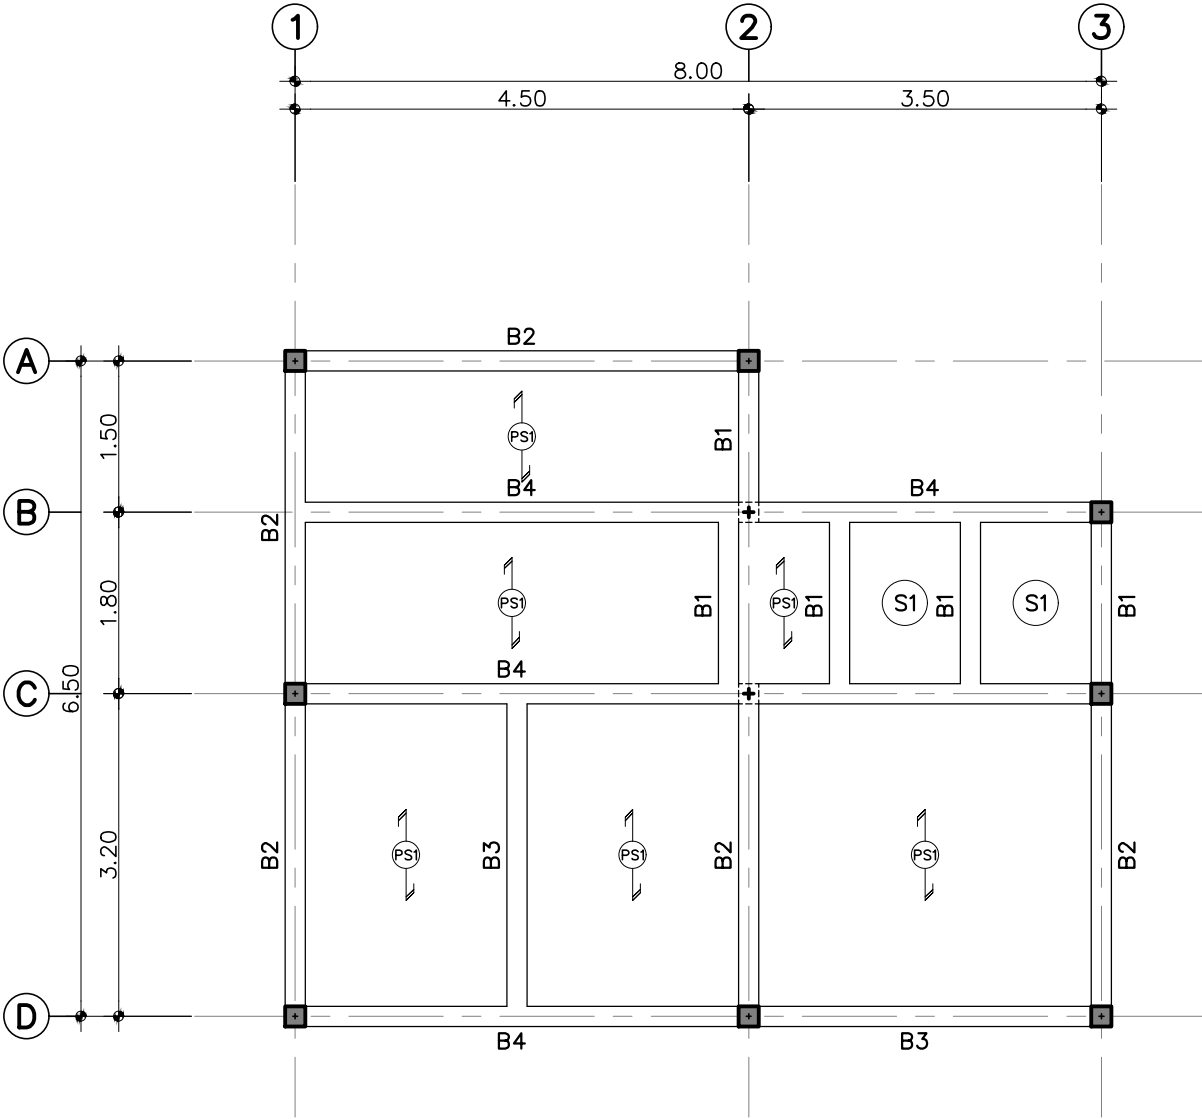


แปลนคานชั้นล่าง

SCALE 1: 75

- หมายเหตุ
- ระดับหลังคานชั้นล่างเท่ากับ +0.45 ม ถ้าไม่ได้ระบุไว้เป็นอย่างอื่น
 - คานรอบนอกที่มีระดับของท้องคานสูงกว่าระดับดิน
ให้เทคريب คสล เสริมใต้ท้องคาน
 - ระดับและระยะของคานและพื้นให้เป็นไปตามแบบสถาปัตยกรรม
พื้นสำเร็จรูปรับน้ำหนักบรรทุกปลอดภัยได้ไม่น้อยกว่า 300 กก./ตร.ม



PROJECT NAME						
สำนักงานนิติบุคคลหมู่บ้านจัดสรร พฤษภา 33						
LOCATION						
ตำบลบางแม่นาง						
อำเภอบางใหญ่ จังหวัดนนทบุรี						
OWNER						
นิติบุคคลหมู่บ้านจัดสรรพฤษภา33						
ARCHITECTS						
-						
-						
-						
ENGINEERS						
TITLE						
แปลนตำแหน่งฐานรากและเสาเข็ม						
แปลนคานชั้นล่าง						
REVISION						
1	2	3	4	5	6	7
DRAWN BY						
DATE	2025-09-01					
DRAWING NO.	TOTAL					
S-07	OF					


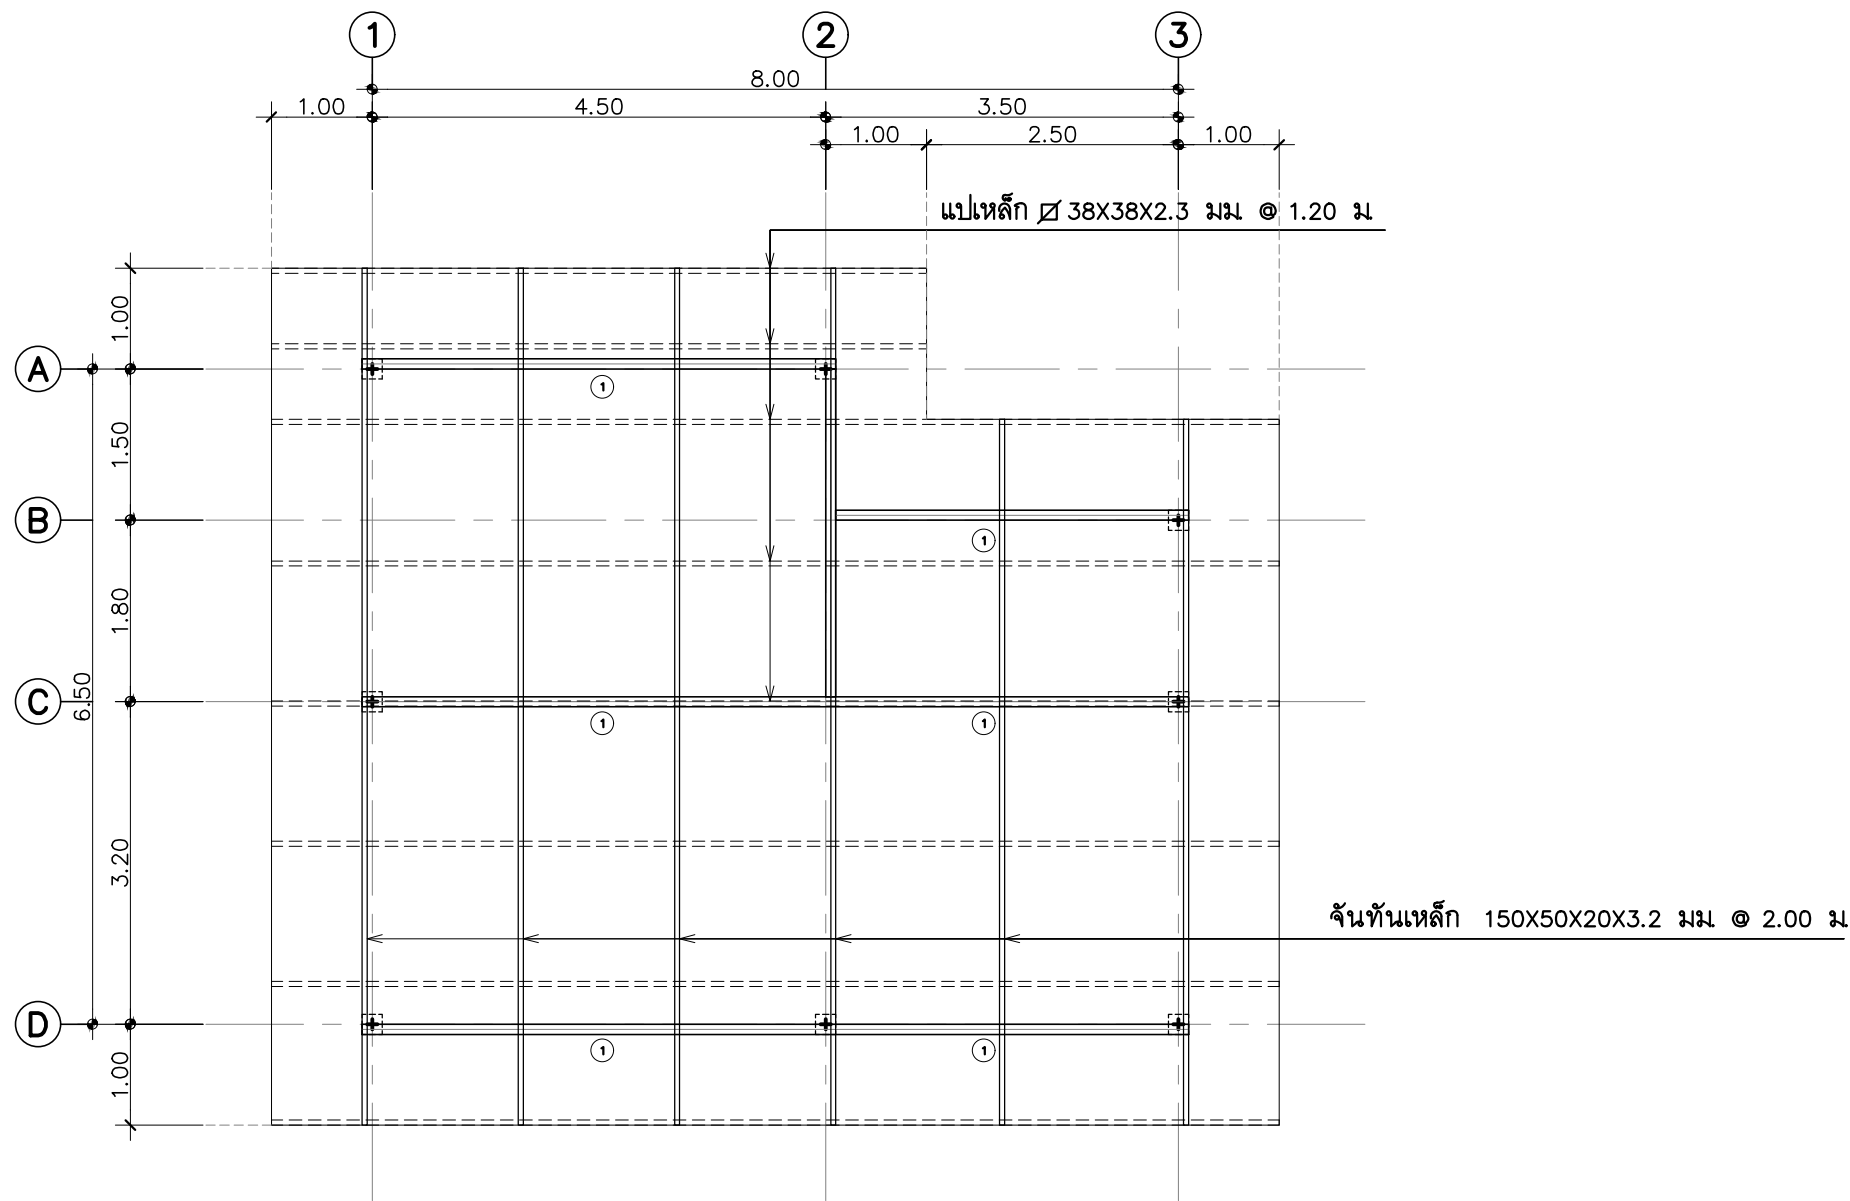


แปลนโครงหลังคา
SCALE 1:100



โครงหลังคาเหล็ก	
MEMBER DESIGNATION	MEMBER SIZE
①	อะเสเหล็ก 2๓ –150X50X20X2.3 มม

REMARK. ระยะและค่าระดับต่างๆให้อิงจากแบบสถาปัตย์เป็นหลัก

PROJECT NAME						
สำนักงานนิติบุคคลหมู่บ้านจัดสรร พฤษภา 33						
LOCATION						
ตำบลบางแม่นาง						
อำเภอบางใหญ่ จังหวัดนนทบุรี						
OWNER						
นิติบุคคลหมู่บ้านจัดสรรพฤษภา33						
ARCHITECTS						
-						
-						
-						
ENGINEERS						
TITLE						
แปลนโครงหลังคา						
REVISION						
1	2	3	4	5	6	7
DRAWN BY						
DATE	2025-09-01					
DRAWING NO.	TOTAL					
S-08	OF					

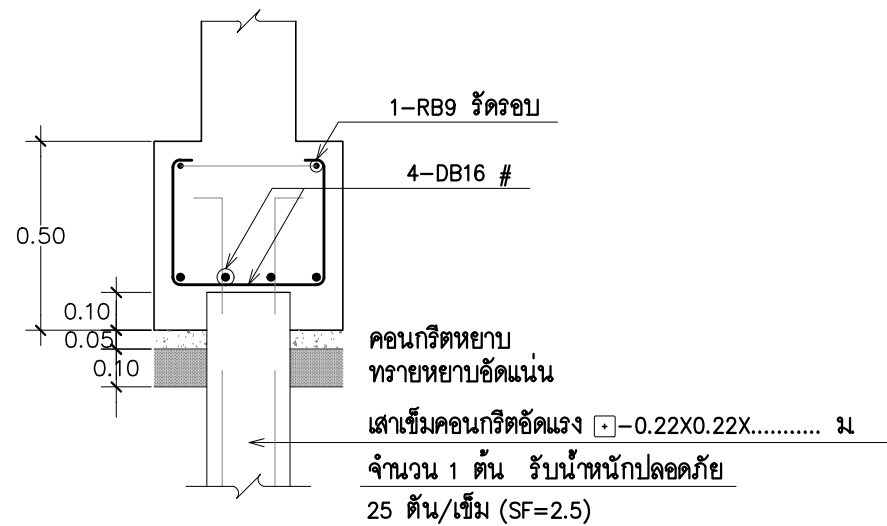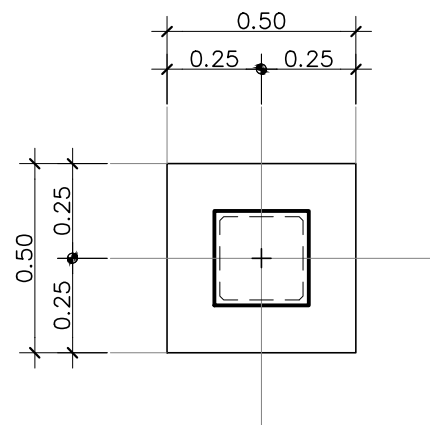



แบบขยายฐานราก F1
SCALE 1: 20

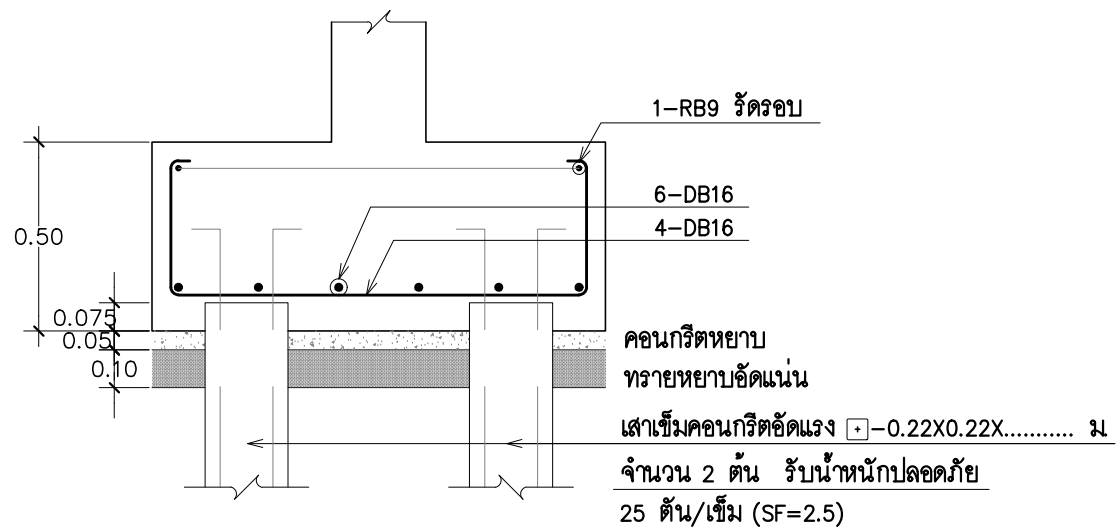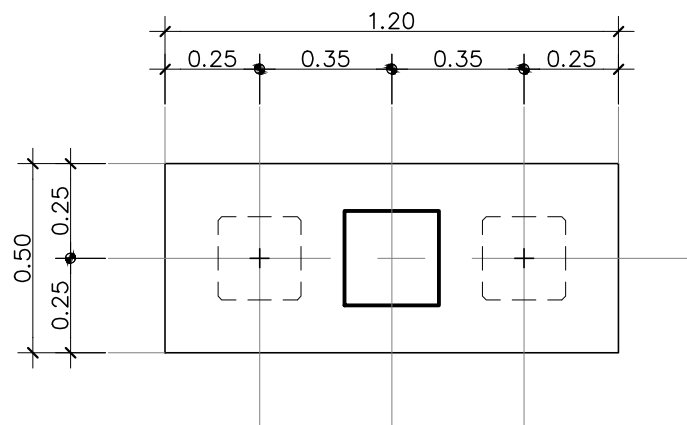


แบบขยายฐานราก F2
SCALE 1: 20

PROJECT NAME						
สำนักงานนิติบุคคลหมู่บ้านจัดสรร พฤษภา 33						
LOCATION						
ตำบลบางแม่นาง						
อำเภอบางใหญ่ จังหวัดนนทบุรี						
OWNER						
นิติบุคคลหมู่บ้านจัดสรรพฤษภา33						
ARCHITECTS						
-						
-						
-						
ENGINEERS						
TITLE						
แบบขยายฐานราก F1-F2						
REVISION						
1	2	3	4	5	6	7
DRAWN BY						
DATE				2025-09-01		
DRAWING NO.				TOTAL		
S-09				OF		


COLUMN		C-I
FLOOR		
ROOF	↑	 0.20X0.20 m. 4DB16 RB6 @ 0.15, TIES
1ST. FLOOR	↑	 0.25X0.25 m. 8DB16 2RB6 @ 0.10, TIES
FOOTING		

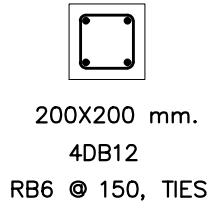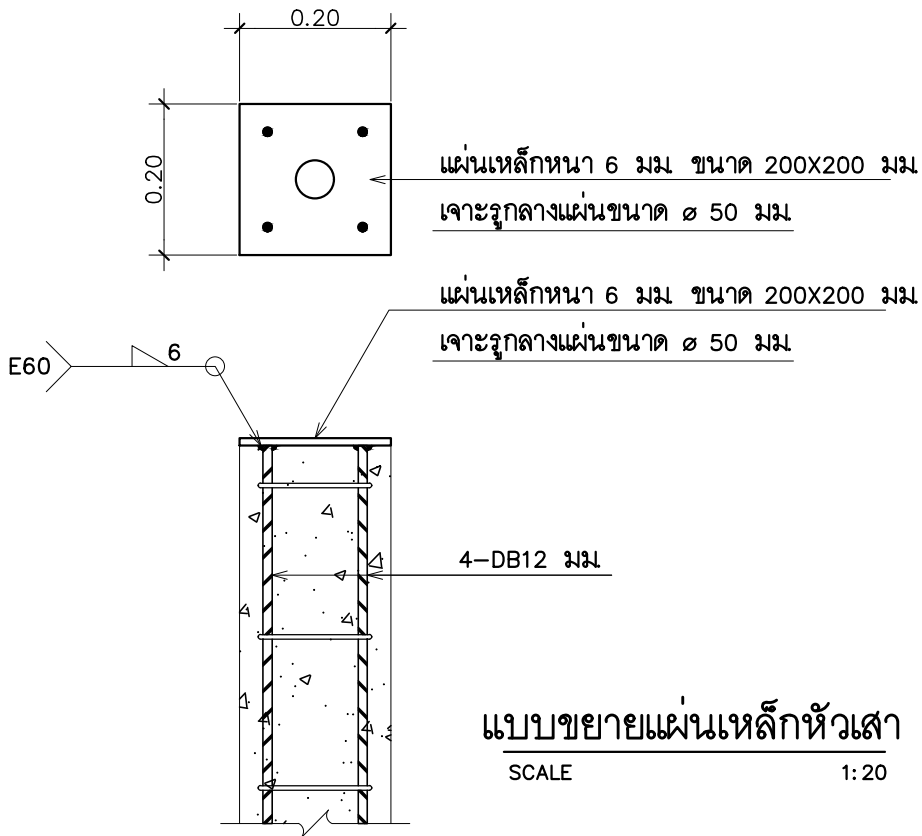


CX

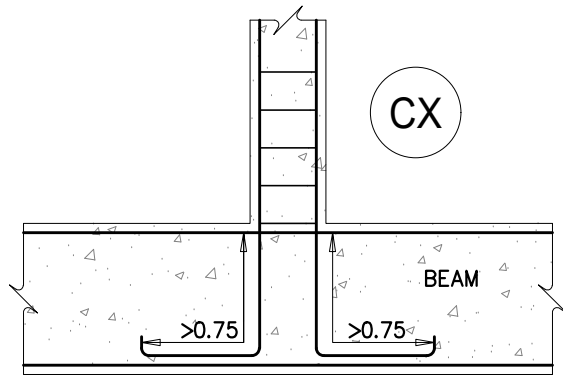

PROJECT NAME						
สำนักงานนิติบุคคลหมู่บ้านจัดสรร พฤษา 33						
LOCATION						
ตำบลบางแม่นาง						
อำเภอบางใหญ่ จังหวัดนนทบุรี						
OWNER						
นิติบุคคลหมู่บ้านจัดสรรพฤษา33						
ARCHITECTS						
-						
-						
-						
ENGINEERS						
TITLE						
แบบขยายเสา C1, CX						
แบบขยายแผ่นเหล็กหัวเสา						
REVISION						
1	2	3	4	5	6	7
DRAWN BY						
DATE	2025-09-01					
DRAWING NO.	TOTAL					
S-10	OF					

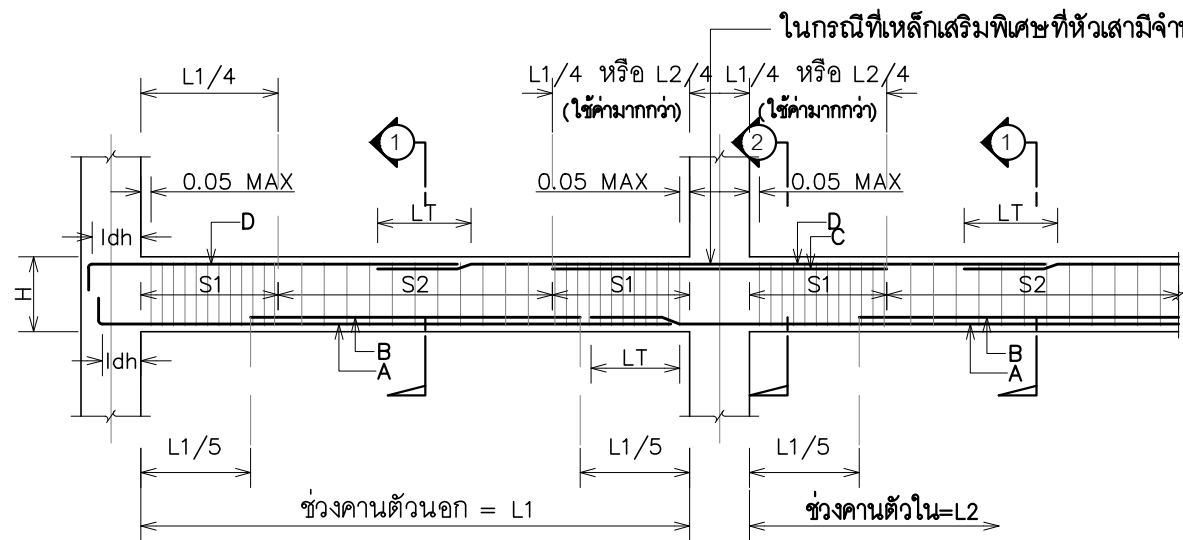


การเสริมเหล็กสำหรับคานต่อเนื่อง TYPE A

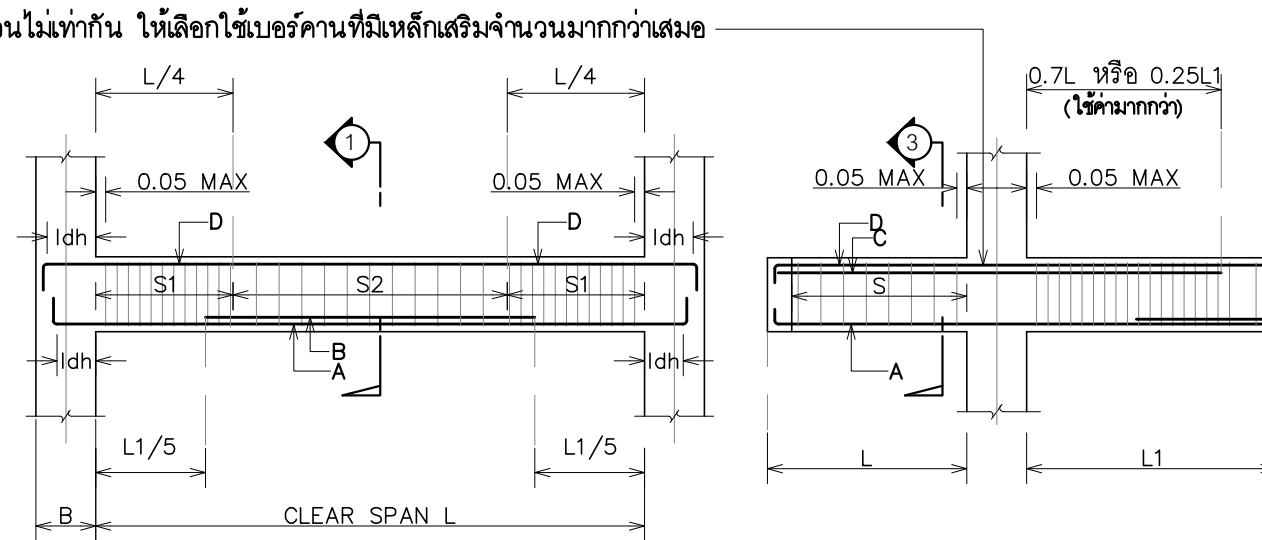


การเสริมเหล็กสำหรับคานช่วงเดียว


การเสริมเหล็กสำหรับคานยื่น TYPE A

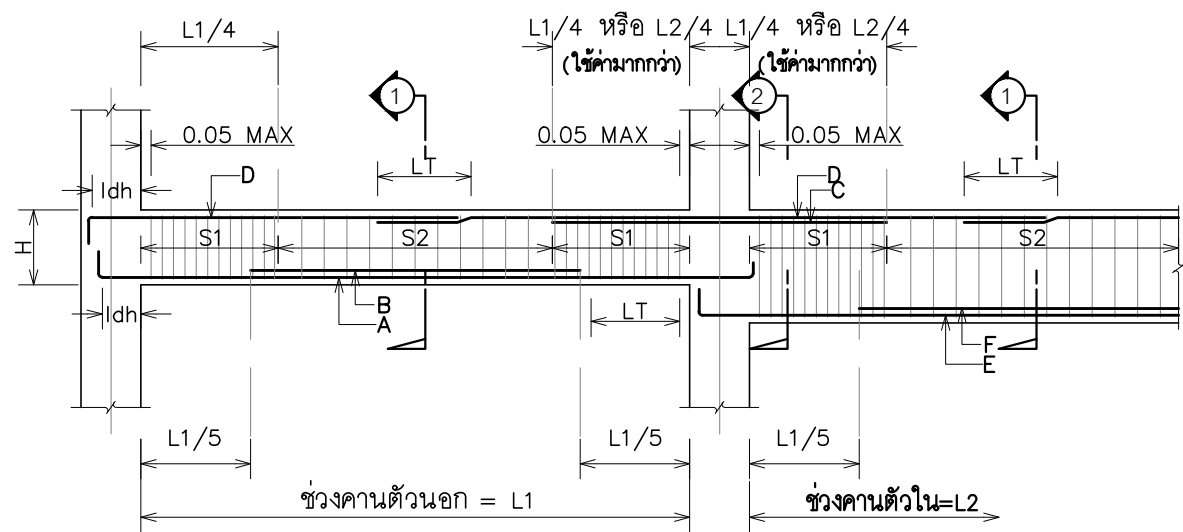

การเสริมเหล็กสำหรับคานต่อเนื่อง TYPE B

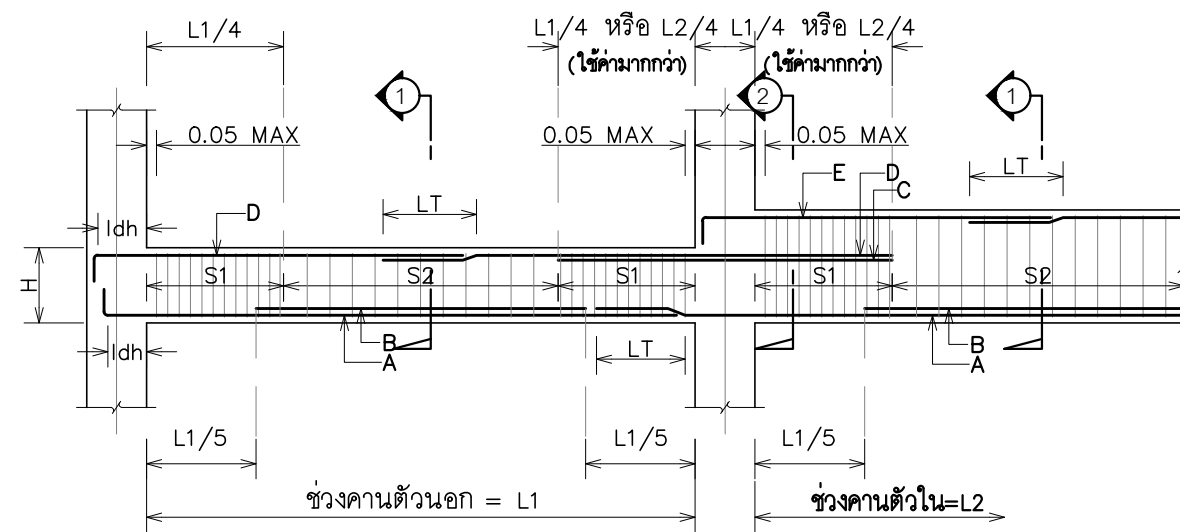


การเสริมเหล็กสำหรับคานต่อเนื่อง TYPE C

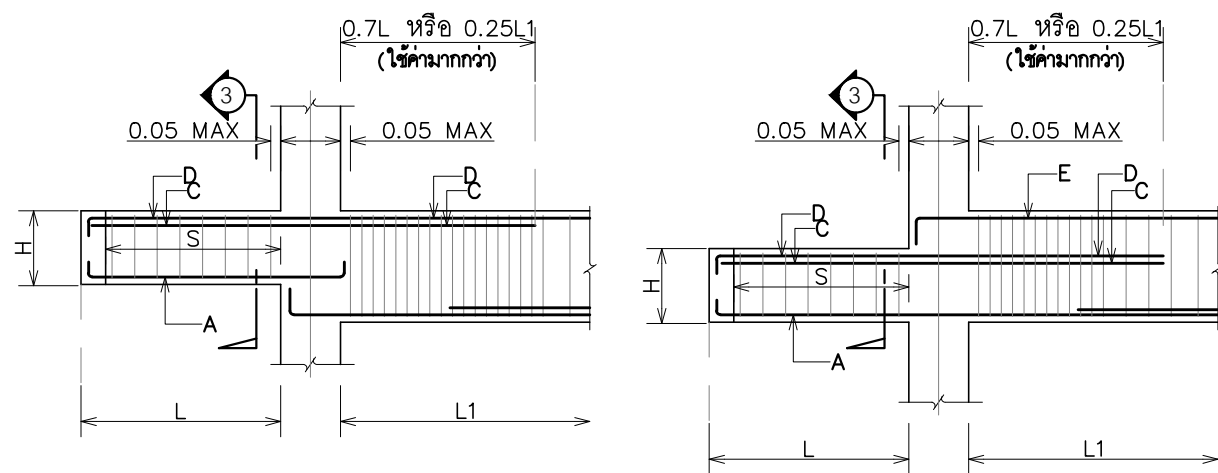


การเสริมเหล็กสำหรับคานยื่น TYPE B

การเสริมเหล็กสำหรับคานยื่น TYPE C

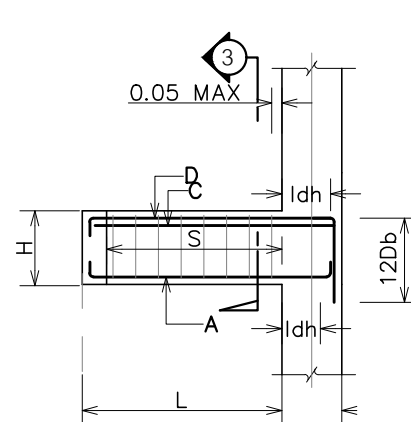

การเสริมเหล็กสำหรับคานยื่น TYPE D



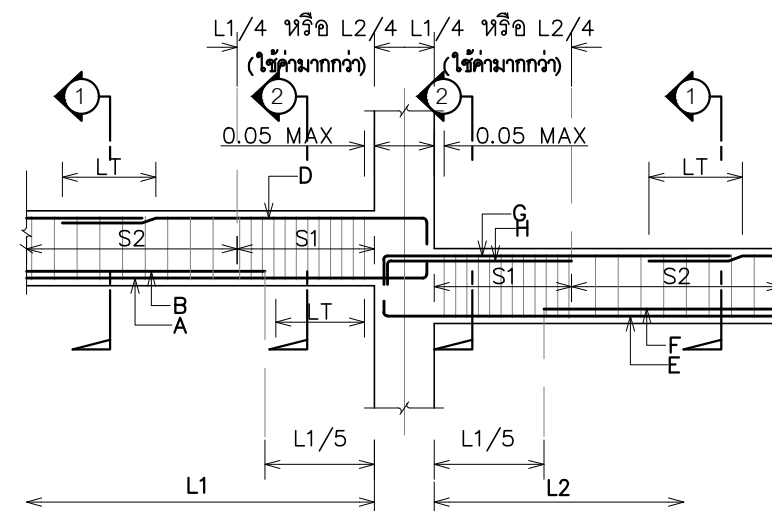


การเสริมเหล็กสำหรับคานต่างระดับ


LT = ระยะต่อทาบเหล็กเสริมในโครงสร้างให้เป็นไปตามมาตรฐานการเสริมเหล็ก
Idh = ระยะฝังยึดเหล็กเสริมในคานต้องมีความลึกไม่น้อยกว่า 15 ซม
12Db = 12 เท่าของขนาดเส้นผ่านศูนย์กลางกลางเหล็กเสริมที่มีขนาดโตสุด

ถ้าไม่ระบุให้ใช้ระยะหุ้มคอนกรีตสำหรับคาน เท่ากัน 3 ซม และเท่ากับ 5 ซม ในกรณีที่สัมผัสกับดิน หรือถูกแดดฝน
ในกรณีที่สัมผัสกับดิน หรือถูกแดดฝน


PROJECT NAME						
สำนักงานนิติบุคคลหมู่บ้านจัดสรร พฤษภา 33						
LOCATION						
ตำบลบางแม่นาง						
อำเภอบางใหญ่ จังหวัดนนทบุรี						
OWNER						
นิติบุคคลหมู่บ้านจัดสรรพฤษภา33						
ARCHITECTS						
-						
-						
-						
ENGINEERS						
TITLE						
มาตรฐานการเสริมเหล็กคาน						
REVISION						
1	2	3	4	5	6	7
DRAWN BY						
DATE	2025-09-01					
DRAWING NO.	TOTAL					
S-11	OF					

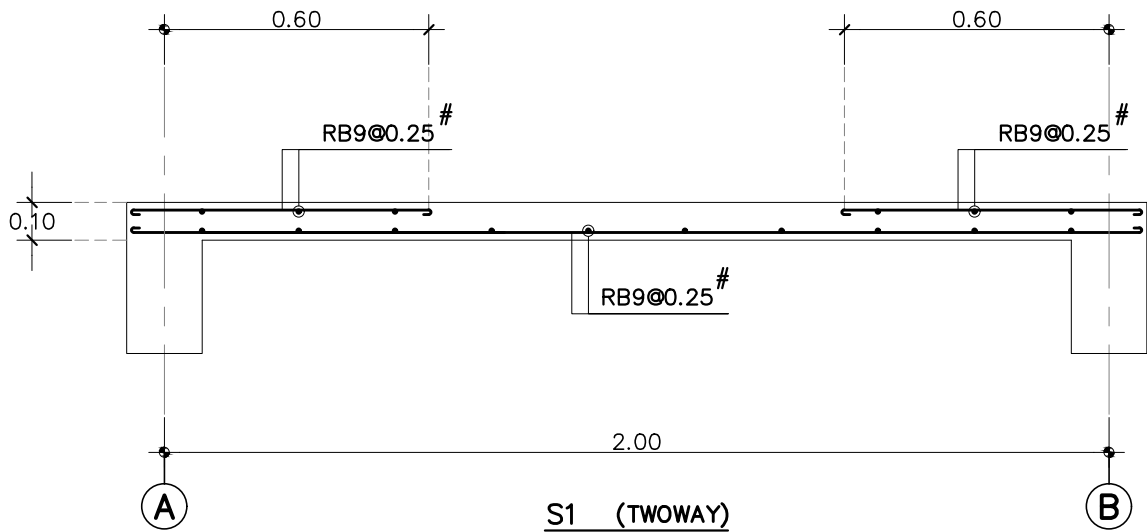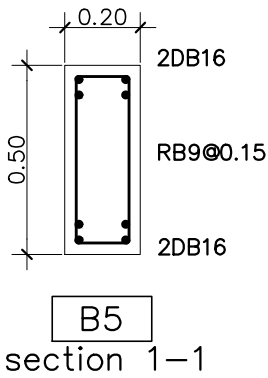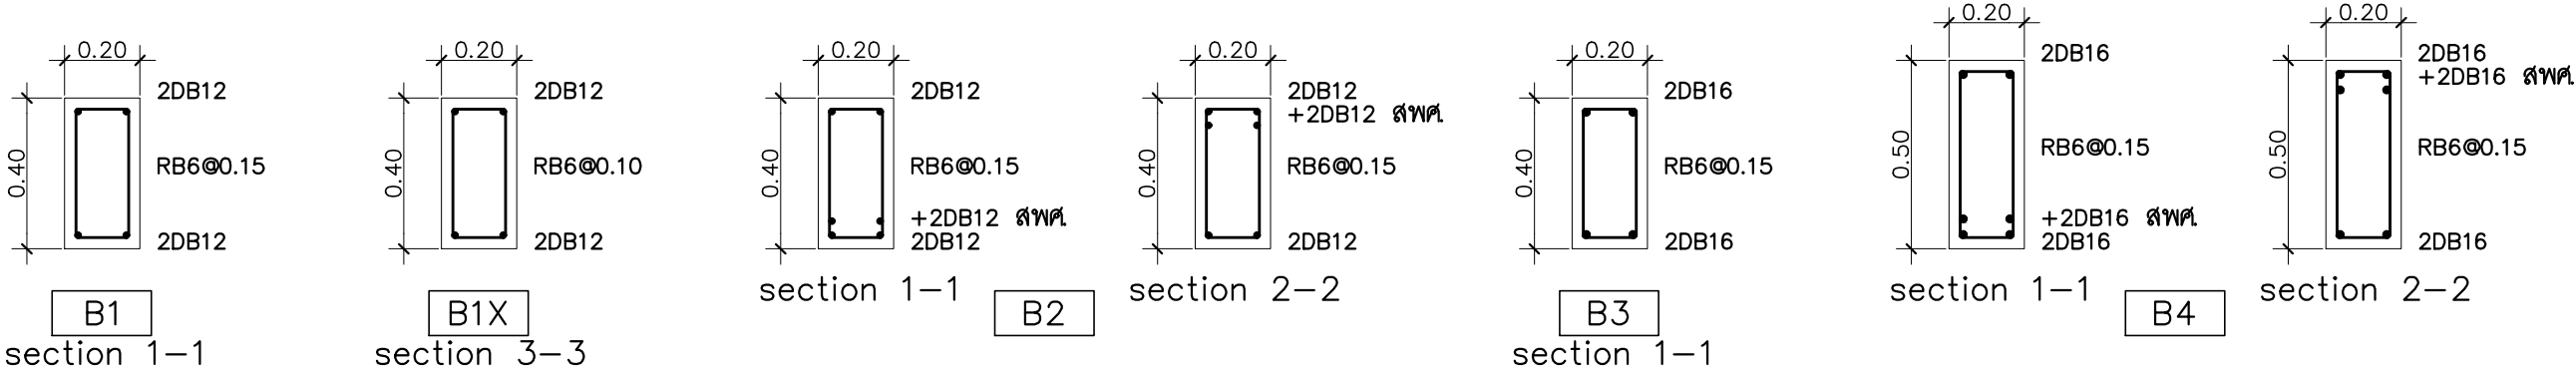


SECTION S1-S1
SCALE 1: 20

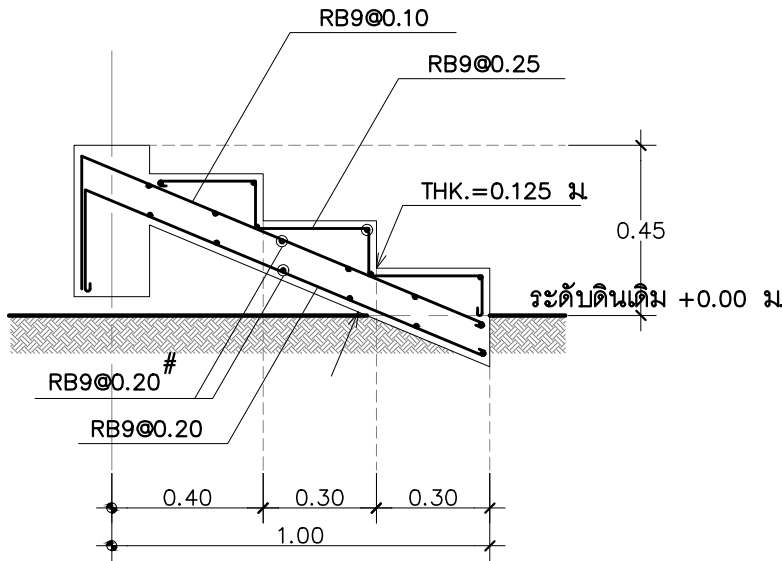

PROJECT NAME						
สำนักงานนิติบุคคลหมู่บ้านจัดสรร พฤษา 33						
LOCATION						
ตำบลบางแม่นาง						
อำเภอบางใหญ่ จังหวัดนนทบุรี						
OWNER						
นิติบุคคลหมู่บ้านจัดสรรพฤษา33						
ARCHITECTS						
-						
-						
-						
ENGINEERS						
TITLE						
แบบขยายโครงสร้างคาน, พื้น, บันได						
REVISION						
1	2	3	4	5	6	7
DRAWN BY						
DATE	2025-09-01					
DRAWING NO.	TOTAL					
S-12	OF					

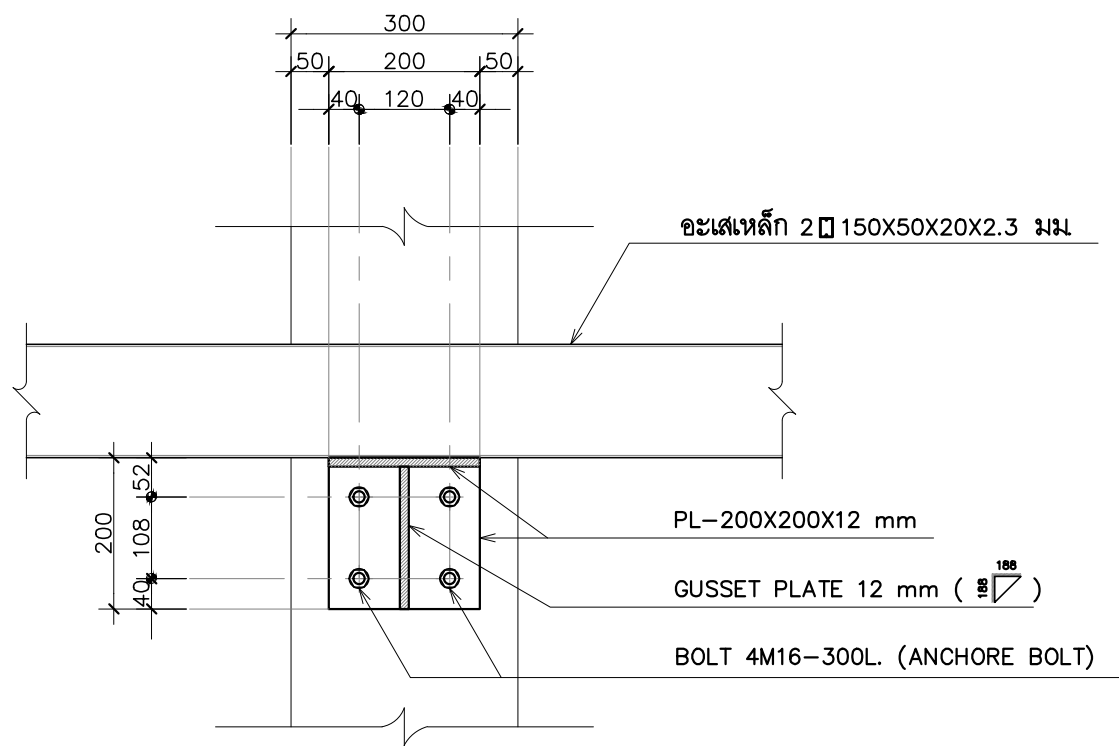


PLAN "J1"

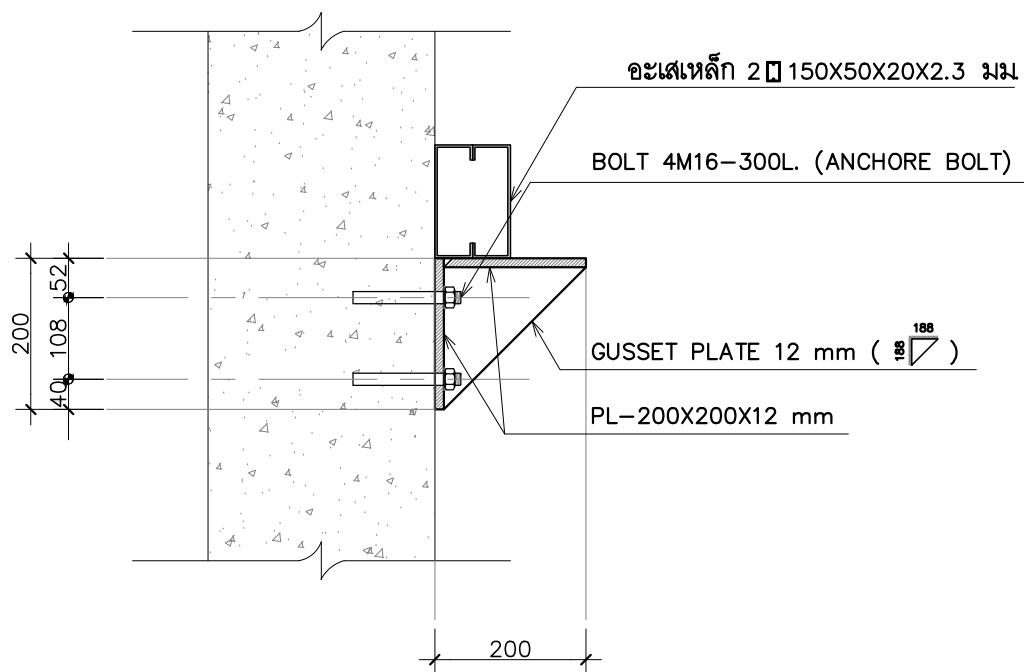


แบบขยายจุดต่อ "J1"

SCALE 1:10


PROJECT NAME						
สำนักงานนิติบุคคลหมู่บ้านจัดสรร พฤษา 33						
LOCATION						
ตำบลบางแม่นาง						
อำเภอบางใหญ่ จังหวัดนนทบุรี						
OWNER						
นิติบุคคลหมู่บ้านจัดสรรพฤษา33						
ARCHITECTS						
-						
-						
-						
ENGINEERS						
TITLE						
แบบขยายจุดต่อ "J1"						
REVISION						
1	2	3	4	5	6	7
DRAWN BY						
DATE		2025-09-01				
DRAWING NO.		TOTAL				
S-13		OF				

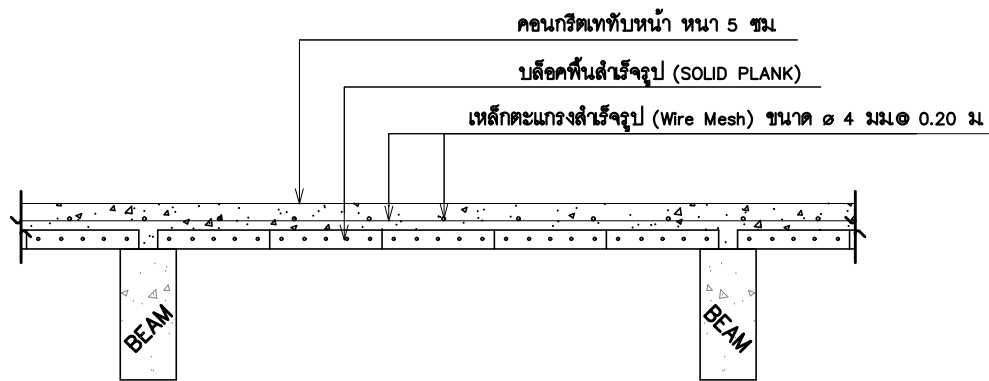


แบบขยายรูปตัดพื้นสำเร็จ (SOLID PLANK) รูปตามขวาง

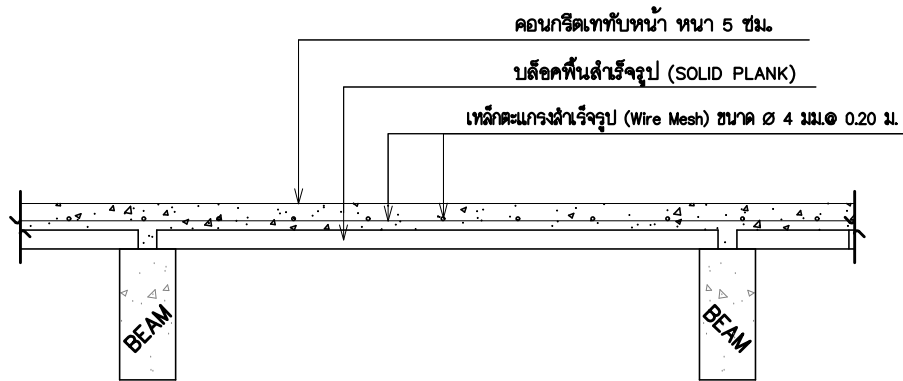


แบบขยายรูปตัดพื้นสำเร็จ (SOLID PLANK) รูปตามยาว

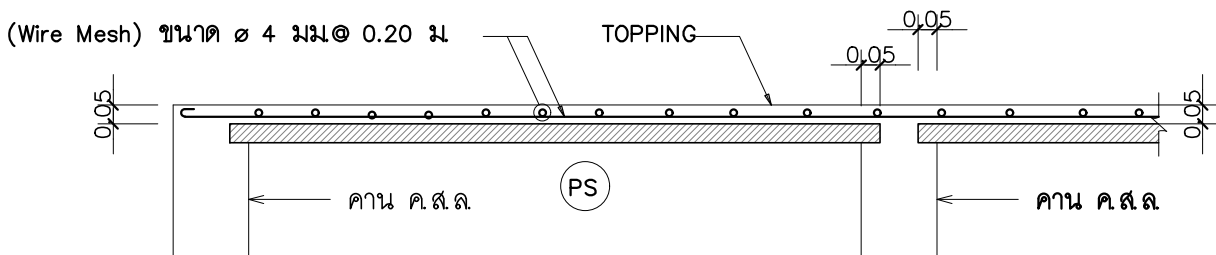


ขยายพื้น TOPPING 1:20

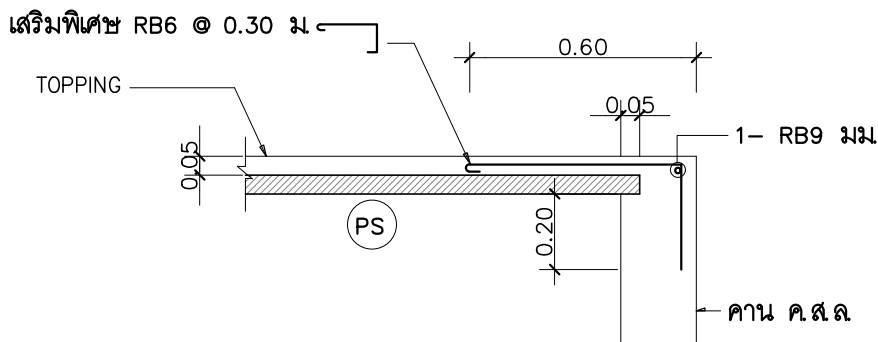


ขยายการวางพื้น (PS) บริเวณคานริม 1:20

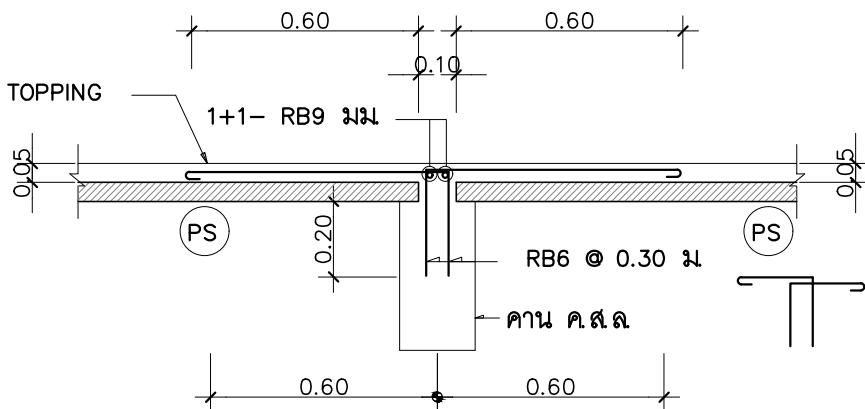


ขยายการวางพื้น (PS) ช่วงภายใน 1:20

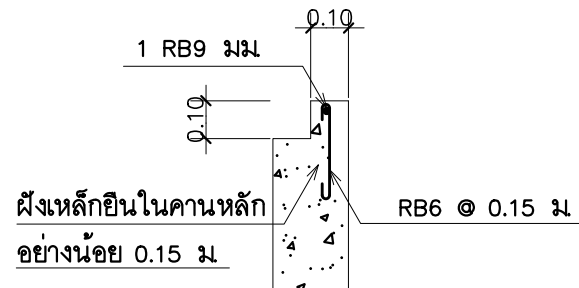

แบบขยายคาน ค.ส.ล. รับพื้นหล่อในที่

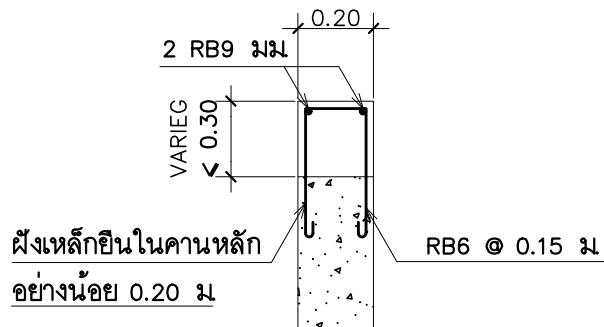

แบบขยายคาน ค.ส.ล. รับพื้นหล่อในที่

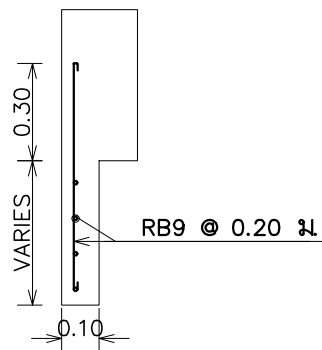


(เสริมใต้คาน)


แบบขยายคาน ค.ส.ล.

PROJECT NAME						
สำนักงานนิติบุคคลหมู่บ้านจัดสรร พฤษภา 33						
LOCATION						
ตำบลบางแม่นาง						
อำเภอบางใหญ่ จังหวัดนนทบุรี						
OWNER						
นิติบุคคลหมู่บ้านจัดสรรพฤษภา33						
ARCHITECTS						
-						
-						
-						
ENGINEERS						
TITLE						
แบบขยายพื้นสำเร็จรูป						
REVISION						
1	2	3	4	5	6	7
DRAWN BY						
DATE	2025-09-01					
DRAWING NO.	TOTAL					
S-14	OF					


แบบขยายรายละเอียดทั่วไปแสดงการยึดและการเชื่อมโครงหลังคาเหล็ก

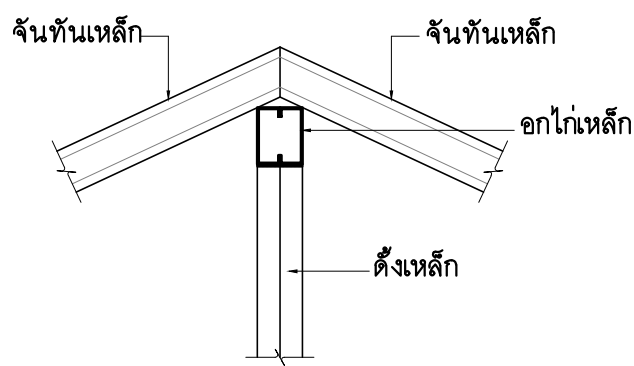


แบบขยาย : การยึดจันทันเหล็กกับอกไก่เหล็ก

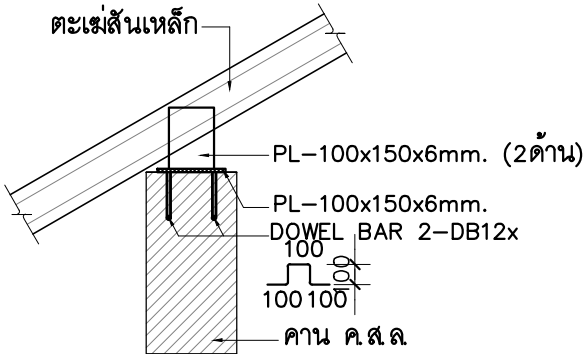


แบบขยาย : การยึดตะแคงเหล็กกับคาน ค.ส.ล.

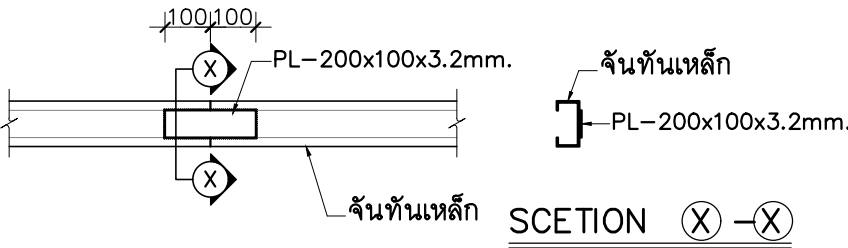


แบบขยาย : การต่อเหล็กจันทัน

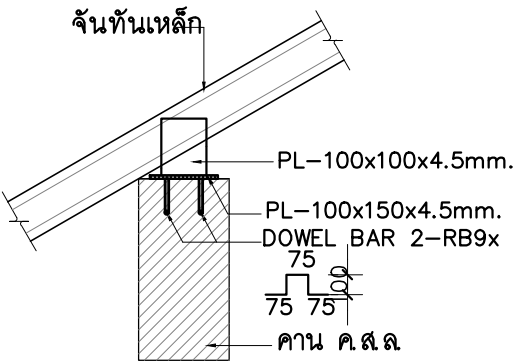

แบบขยาย : การยึดจันทันเหล็กกับคาน ค.ส.ล.

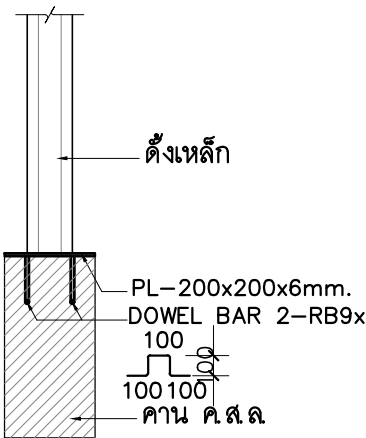


แบบขยาย : การยึดดั่งเหล็กกับคาน ค.ส.ล.

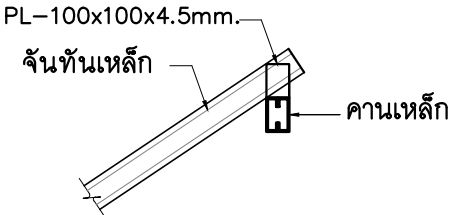

แบบขยาย : การยึดจันทันกับคานเหล็ก


NOTE : เชื่อมรอบขนาด 3mm. (E60) (MINIMUM)

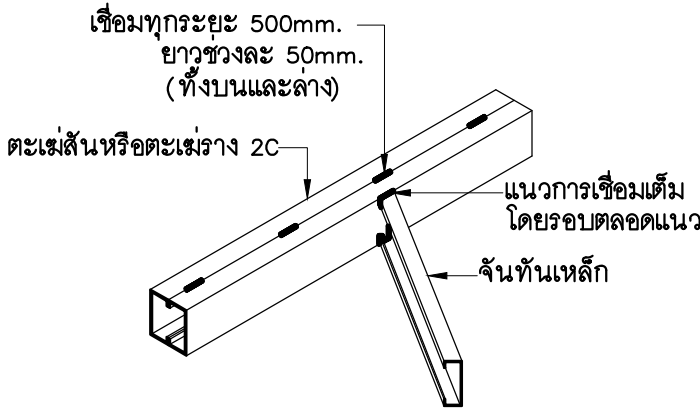

หมายเหตุ

กรณีเชื่อมชนจันทันจะต้องแนบกับตะแคงหรือห่างไม่เกิน 3 มม ถ้าห่างเกินให้ใช้เหล็กฉาก 25x25x3 มม. เชื่อมทาบตามแนวเดิมทั้ง 2 ด้าน


แบบขยาย : การเชื่อมจันทันชนตะแคง

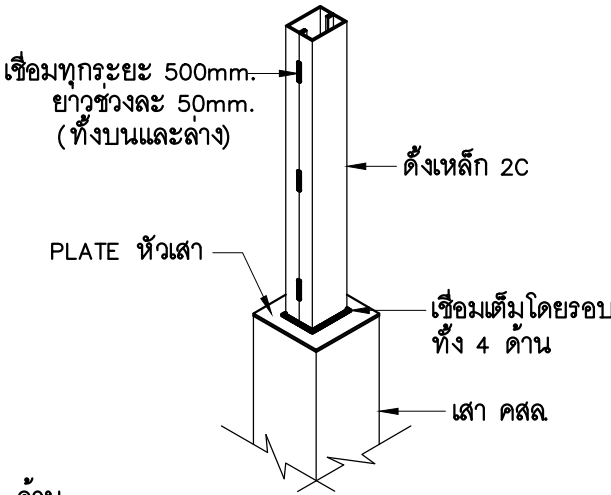


แบบขยาย : การวางดั่งบนเสา คสล.

PROJECT NAME						
สำนักงานนิติบุคคลหมู่บ้านจัดสรร พฤษา 33						
LOCATION						
ตำบลบางแม่นาง						
อำเภอบางใหญ่ จังหวัดนนทบุรี						
OWNER						
นิติบุคคลหมู่บ้านจัดสรรพฤษา33						
ARCHITECTS						
-						
-						
-						
ENGINEERS						
-						
-						
-						
TITLE						
แบบขยายการเชื่อมโครงหลังคา 1						
REVISION						
1	2	3	4	5	6	7
DRAWN BY						
DATE		2025-09-01				
DRAWING NO.		TOTAL				
S-15		OF				


แบบขยายรายละเอียดทั่วไปแสดงการยึดและการเชื่อมโครงหลังคาเหล็ก

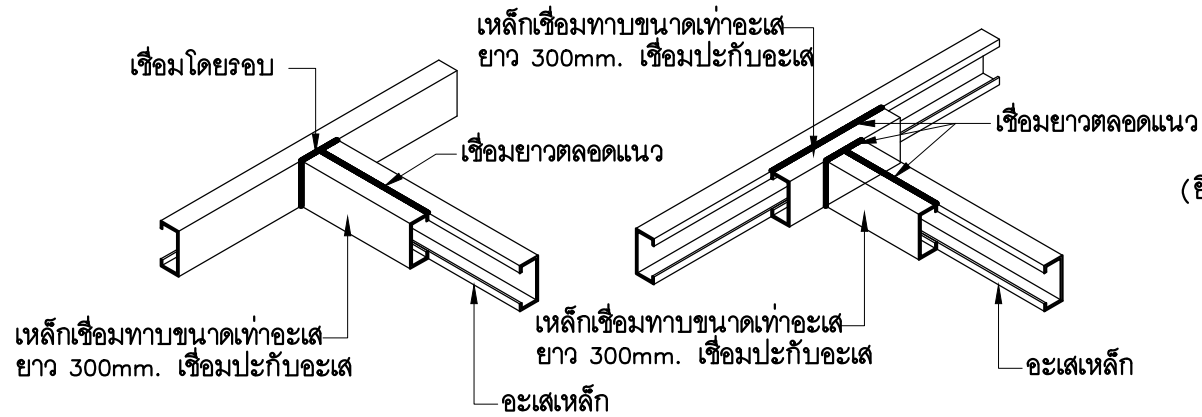


แบบขยาย :
การเชื่อมชนอะเสเหล็ก

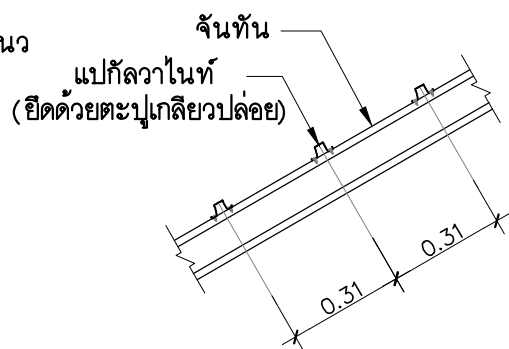

แบบขยาย :
การติดตั้งแป็กฉวไนท์

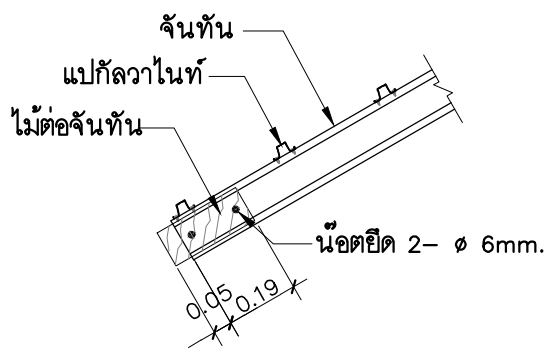

แบบขยายไม่รับเชิงชาย

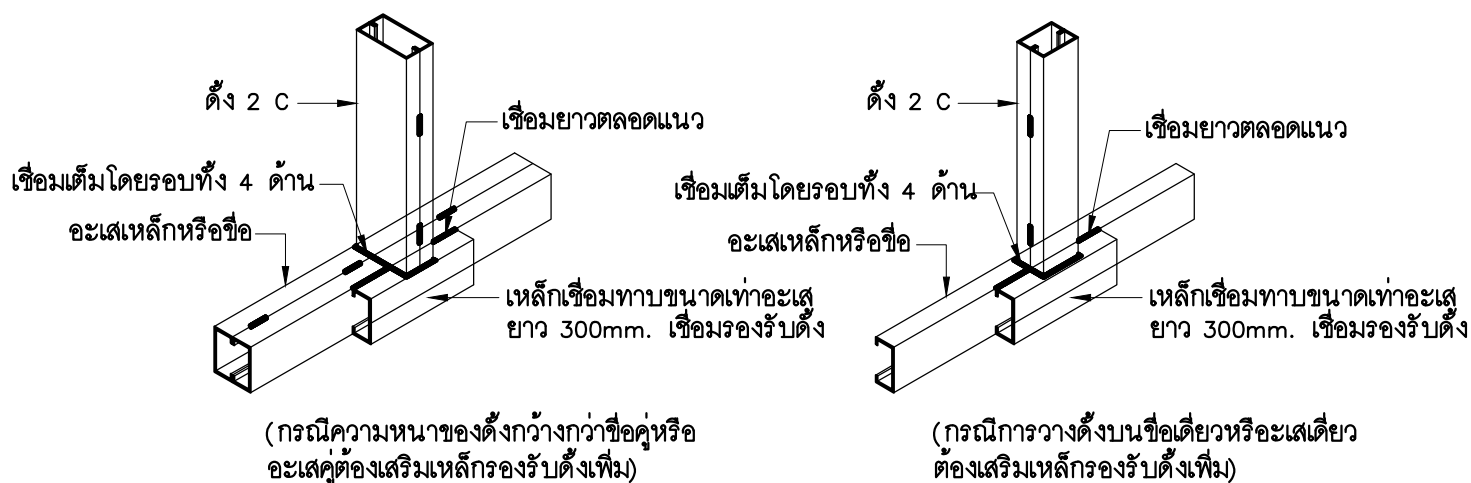



แบบขยาย :
การวางดิ่งบนอะเส

PROJECT NAME						
สำนักงานนิติบุคคลหมู่บ้านจัดสรร ทฤษฎา 33						
LOCATION						
ตำบลบางแม่นาง						
อำเภอบางใหญ่ จังหวัดนนทบุรี						
OWNER						
นิติบุคคลหมู่บ้านจัดสรรทฤษฎา33						
ARCHITECTS						
-						
-						
-						
ENGINEERS						
TITLE						
แบบขยายการเชื่อมโครงหลังคา 2						
REVISION						
1	2	3	4	5	6	7
DRAWN BY						
DATE				2025-09-01		
DRAWING NO.				TOTAL		
S-16				OF		

งานไฟฟ้า ¹	รายละเอียด
สายเมน	สายเดี่ยว ขนาด 16 มม. ความยาวไม่เกิน 20 เมตร จากผนังด้านนอกอาคาร (มาตรฐาน มอก.) (เดินลอย)
มิเตอร์ไฟฟ้า	15/45 Amp. 2 สาย
สายไฟภายในบ้าน	(มาตรฐาน มอก.) ร้อยท่อ PVC ผึงผนัง
ลูกย้อยสวิตช์ตัดตอนอัตโนมัติ	2 จุด
สายไฟฟ้าแสงสว่าง (สวิตช์)	เส้นผ่าศูนย์กลาง 1.5 มิลลิเมตร (มาตรฐาน มอก.)
สายไฟฟ้ากำลัง (ปลั๊ก)	เส้นผ่าศูนย์กลาง 2.5 มิลลิเมตร (มาตรฐาน มอก.)
อุปกรณ์ปลั๊กสวิตช์	ยี่ห้อ CHANG (มาตรฐาน มอก.)
แผงควบคุมสวิตช์ไฟฟ้า	ยี่ห้อ CHANG (มาตรฐาน มอก.)
ดวงโคม	32 Watts (ตามราคารามาตรฐานบริษัท) ราคา 300 บาท/ชุด

¹ ไม่รวมค่าธรรมเนียมส่วนราชการ


รายการประกอบแบบไฟฟ้า (ตำแหน่งตามความเหมาะสมที่หน้างาน)			
สัญลักษณ์	รายละเอียด	สัญลักษณ์	รายละเอียด
	แผงสวิตช์และคัตเอาท์		ตำแหน่งไฟกิ่ง
	ตำแหน่งสวิตช์ 1 ตัวใน 1 ตลับ		ตำแหน่งโคมไฟ 32 วัตต์
	ตำแหน่งสวิตช์ 2 ทาง		ดวงโคมฟลูออเรสเซนต์ ติดได้ผ้า 20 วัตต์
	เต้าเสียบปลั๊ก ชนิดฝัง		เต้าเสียบปลั๊ก ชนิดกันน้ำใช้ภายนอก

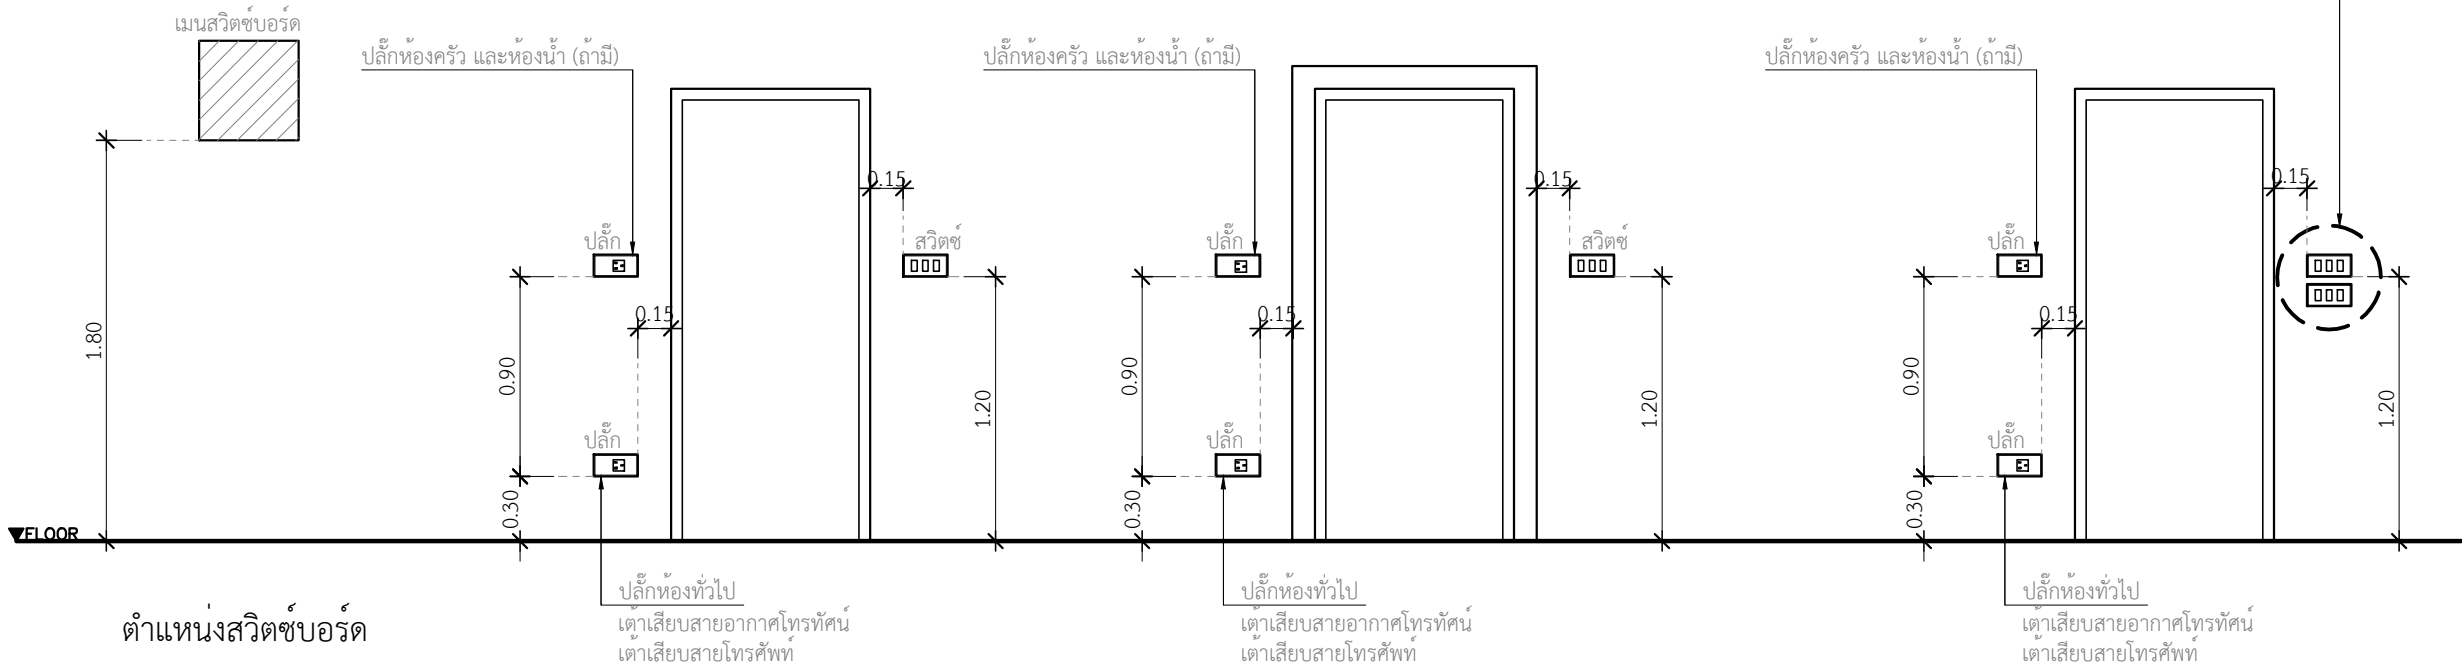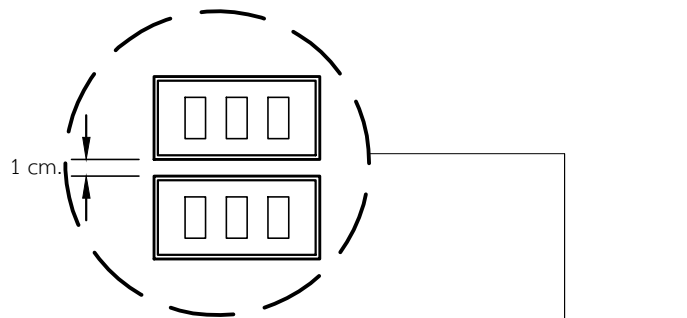

ตำแหน่งสวิตช์และปลั๊กทั่วไป

หมายเหตุ : มาตรฐานความเข้มของแสงสว่างภายในอาคาร ไม่น้อยกว่า 100 ลักซ์ (LUX)
ยี่ตระดับปลั๊กไฟไว้ที่ +0.30 จากพื้น หากไม่ได้ระบุไว้เป็นระดับอื่น

PROJECT NAME						
สำนักงานนิติบุคคลหมู่บ้านจัดสรร ทฤษฎา 33						
LOCATION						
ตำบลบางแม่นาง						
อำเภอบางใหญ่ จังหวัดนนทบุรี						
OWNER						
นิติบุคคลหมู่บ้านจัดสรรทฤษฎา33						
ARCHITECTS						
-						
-						
-						
ENGINEERS						
-						
-						
-						
TITLE						
รายการประกอบแบบไฟฟ้า						
-						
REVISION						
1	2	3	4	5	6	7
DRAWN BY						
-						
.						
DATE	2025-09-01					
DRAWING NO.	TOTAL					
EE-01	OF					

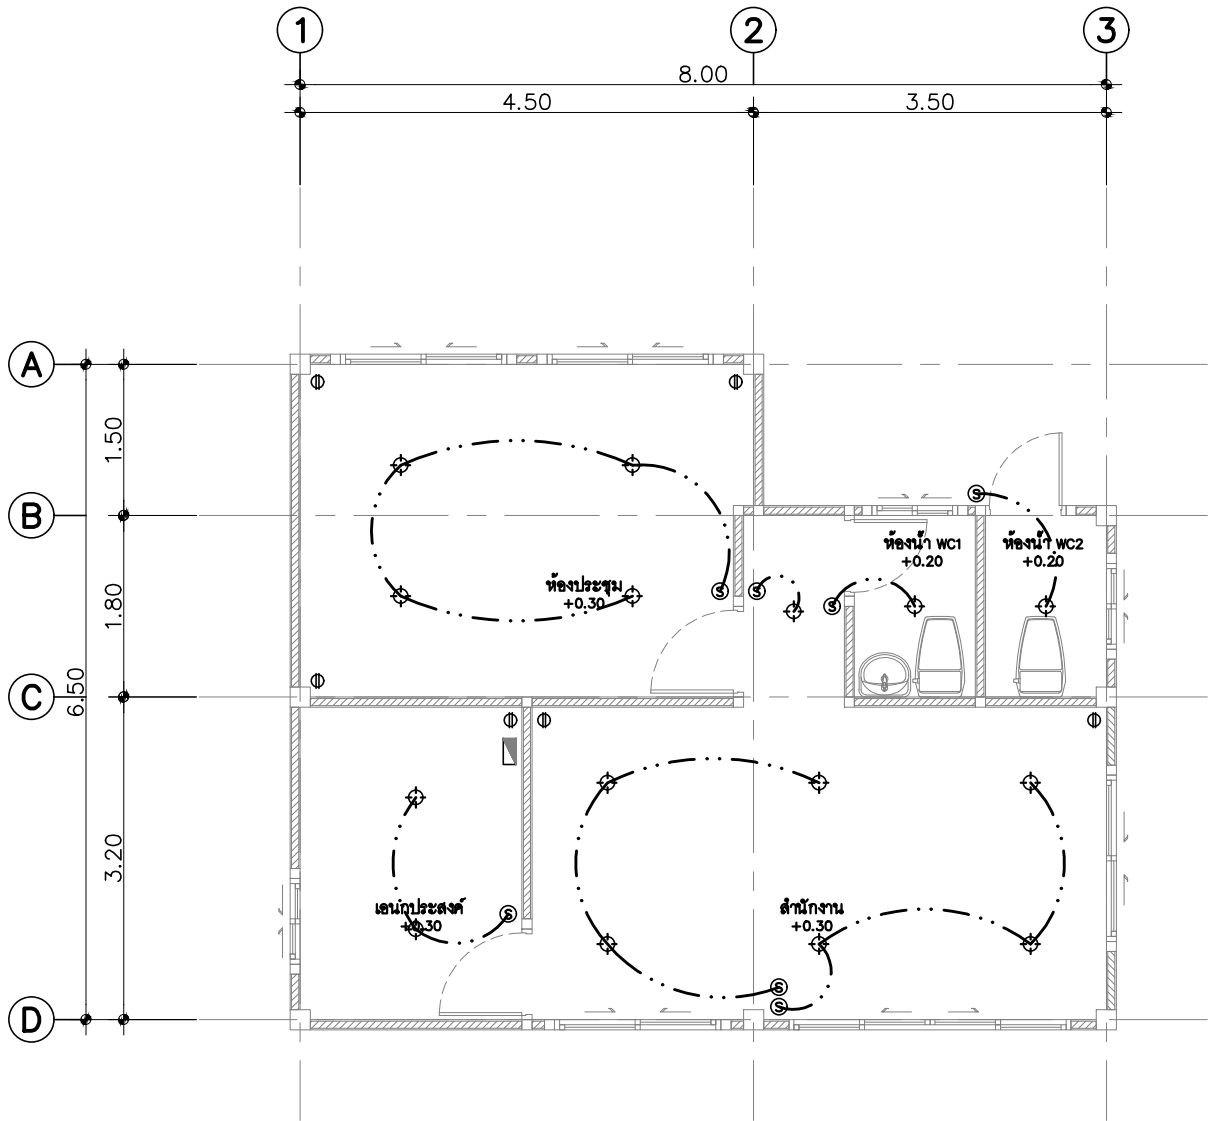

ผังไฟฟ้า

มาตราส่วน 1: 75

3
A-303

4
A-304

2
A-302




1
A-301

งานไฟฟ้า ¹	รายละเอียด
สายเมน	สายเดี่ยว ขนาด 16 มม. ความยาวไม่เกิน 20 เมตร จากหนึ่งคานนอกอาคาร (มาตรฐาน มอก.) (เดินลอย)
มิเตอร์ไฟฟ้า	15/45 Amp. 2 สาย
สายไฟภายในบ้าน	(มาตรฐาน มอก.) ร้อยท่อ PVC มังเหล่ง
ลูกยายสวิตช์ตัดตอนอัตโนมัติ	2 จุด
สายไฟฟ้าแสงสว่าง (สวิตช์)	เส้นผ่าศูนย์กลาง 1.5 มิลลิเมตร (มาตรฐาน มอก.)
สายไฟฟ้ากำลัง (ปลั๊ก)	เส้นผ่าศูนย์กลาง 2.5 มิลลิเมตร (มาตรฐาน มอก.)
อุปกรณ์อิเล็กทรอนิกส์	ยี่ห้อ CHANG (มาตรฐาน มอก.)
แผงควบคุมสวิตช์ไฟฟ้า	ยี่ห้อ CHANG (มาตรฐาน มอก.)
ดวงโคม	32 Watts (ตามราคามาตรฐานบริษัท) ราคา 300 บาท/ชุด

¹ ไม่รวมค่าธรรมเนียมส่วนราชการ

หมายเหตุ : มาตรฐานความเข้มของแสงสว่างภายในอาคาร ไม่น้อยกว่า 100 ลักซ์ (LUX)
ยี่ระดับปลั๊กไฟไว้ที่ +0.30 จากพื้น หากไม่ได้ระบุไว้เป็นระดับอื่น

PROJECT NAME						
สำนักงานนิติบุคคลหมู่บ้านจัดสรร พฤษา 33						
LOCATION						
ตำบลบางแม่นาง						
อำเภอบางใหญ่ จังหวัดนนทบุรี						
OWNER						
นิติบุคคลหมู่บ้านจัดสรรพฤษา33						
ARCHITECTS						
-						
-						
-						
ENGINEERS						
TITLE						
ผังไฟฟ้า (ดวงโคม)						
-						
REVISION						
1	2	3	4	5	6	7
DRAWN BY						
-						
.						
DATE	2025-09-01					
DRAWING NO.	TOTAL					
EE-02	OF					

 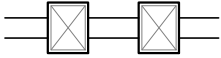 
รายการประกอบแบบสุขาภิบาล	
สัญลักษณ์	รายละเอียด
	ท่อประปา ท่อ PVC ภายนอก Ø 3/4" ภายในชั้น 13.5 Ø 1/2"
	ท่อน้ำทิ้ง ท่อ PVC ชั้น 8.5 Ø 3" ท่อแยกสุขภัณฑ์ Ø1/ 2"
	มิเตอร์น้ำ พร้อมวาล์ว เปิด-ปิด
	ท่อระบายน้ำภายนอกใช้ท่อซีเมนต์ใยหิน Ø 6"
	บ่อพักคอนกรีตสำเร็จรูปพร้อมฝาคอนกรีต ขนาด 0.40x0.30 ม. @ไม่เกิน 6 ม. หรือทุกจุดหักเลี้ยวของบ่อ
	ถังบำบัดน้ำเสีย DOS ULTRA 800
	ท่อน้ำโสโครก ท่อ PVC ชั้น 8.5 Ø 4"
	รูระบายน้ำที่พื้นตะแกรงสแตนเลส 304
	รูระบายน้ำที่หลังคาค.ส.ล. ตะแกรงสแตนเลส 304

**หมายเหตุ รายละเอียดสเปควัสดุงานประปา

งานประปา ¹	รายละเอียด
ท่อเมนประปา	ท่อ PVC ขนาด Ø 6 หุน ชั้น 13.5 ไม่เกิน 20 เมตร
ท่อน้ำดี	ท่อ PVC ขนาด Ø 4 หุน ชั้น 13.5
ท่อน้ำทิ้ง	ท่อ PVC ขนาด Ø 3" ชั้น 8.5
ระบบบำบัดน้ำเสีย	บ่อเกรอะ-บ่อซึม

¹ไม่รวมค่าธรรมเนียมส่วนราชการ

PROJECT NAME						
สำนักงานนิติบุคคลหมู่บ้านจัดสรร ทฤษฎา 33						
LOCATION						
ตำบลบางแม่นาง						
อำเภอบางใหญ่ จังหวัดนนทบุรี						
OWNER						
นิติบุคคลหมู่บ้านจัดสรรทฤษฎา33						
ARCHITECTS						
-						
-						
-						
ENGINEERS						
TITLE						
รายการประกอบแบบสุขาภิบาล						
-						
REVISION						
1	2	3	4	5	6	7
DRAWN BY						
-						
.						
DATE	2025-09-01					
DRAWING NO.	TOTAL					
SN-01	OF					

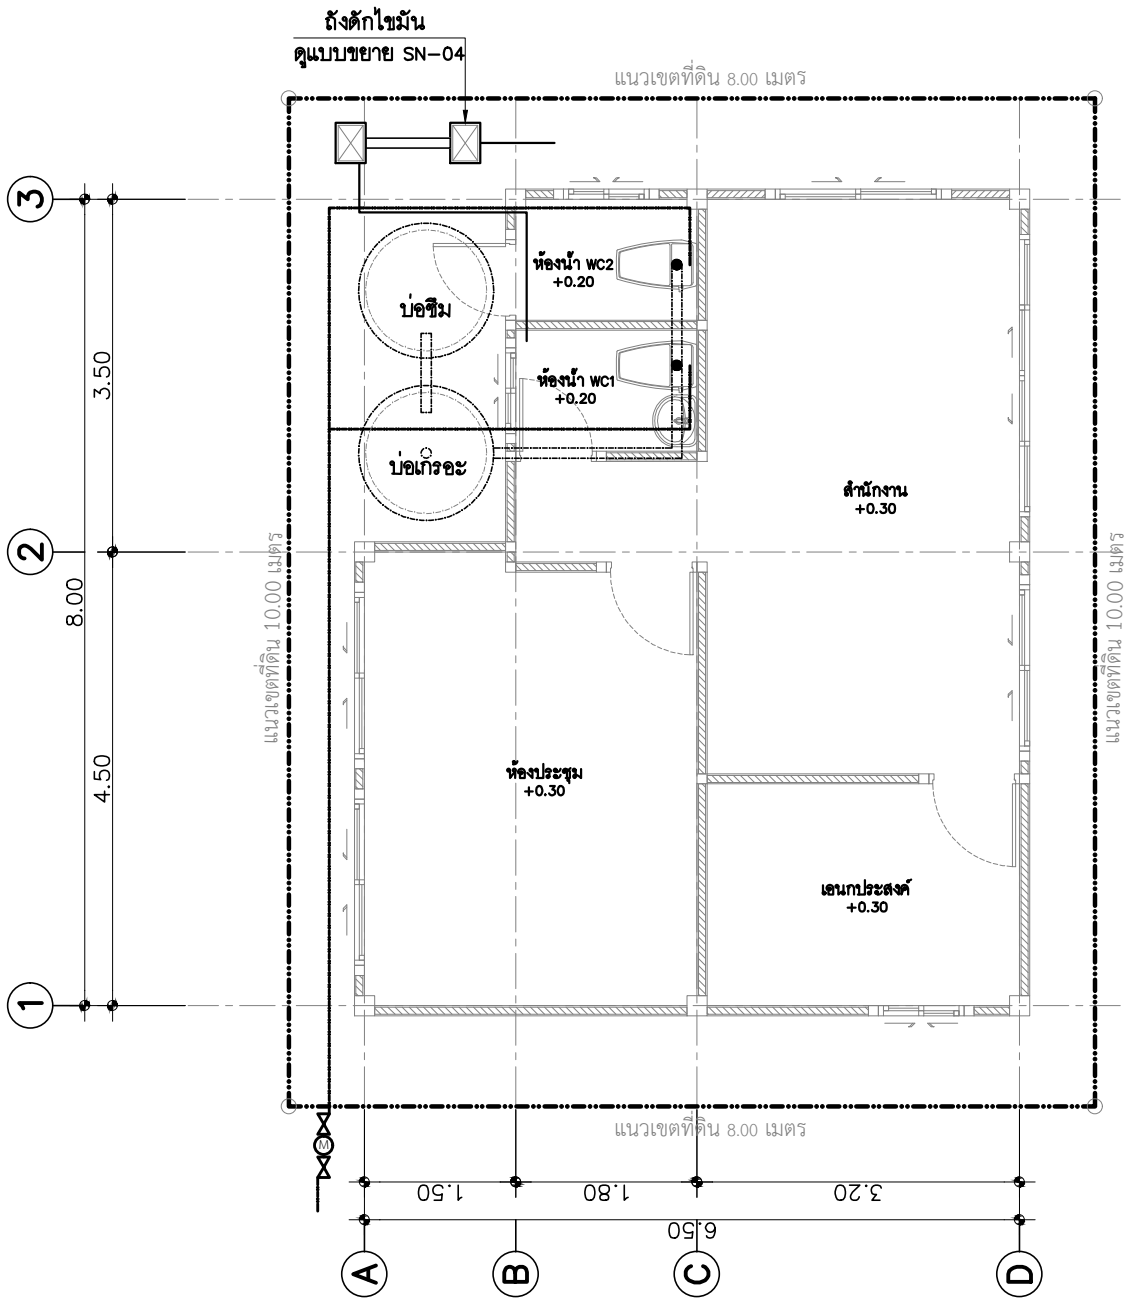


ผังสุขาภิบาล

มาตราส่วน 1: 200

งานประปา ¹	รายละเอียด
ท่อเมนประปา	ท่อ PVC ขนาด Ø 6 หุน ชั้น 13.5 ไม่เกิน 20 เมตร
ท่อน้ำดี	ท่อ PVC ขนาด Ø 4 หุน ชั้น 13.5
ท่อน้ำทิ้ง	ท่อ PVC ขนาด Ø 3" ชั้น 8.5
ระบบบำบัดน้ำเสีย	บ่อเกรอะ-บ่อซึม

¹ไม่รวมค่าธรรมเนียมส่วนราชการ

PROJECT NAME						
สำนักงานนิติบุคคลหมู่บ้านจัดสรร พฤษภา 33						
LOCATION						
ตำบลบางแม่นาง						
อำเภอบางใหญ่ จังหวัดนนทบุรี						
OWNER						
นิติบุคคลหมู่บ้านจัดสรรพฤษภา33						
ARCHITECTS						
-						
-						
-						
ENGINEERS						
TITLE						
ผังสุขาภิบาล						
-						
REVISION						
1	2	3	4	5	6	7
DRAWN BY						
-						
.						
DATE	2025-09-01					
DRAWING NO.	TOTAL					
SN-02	OF					



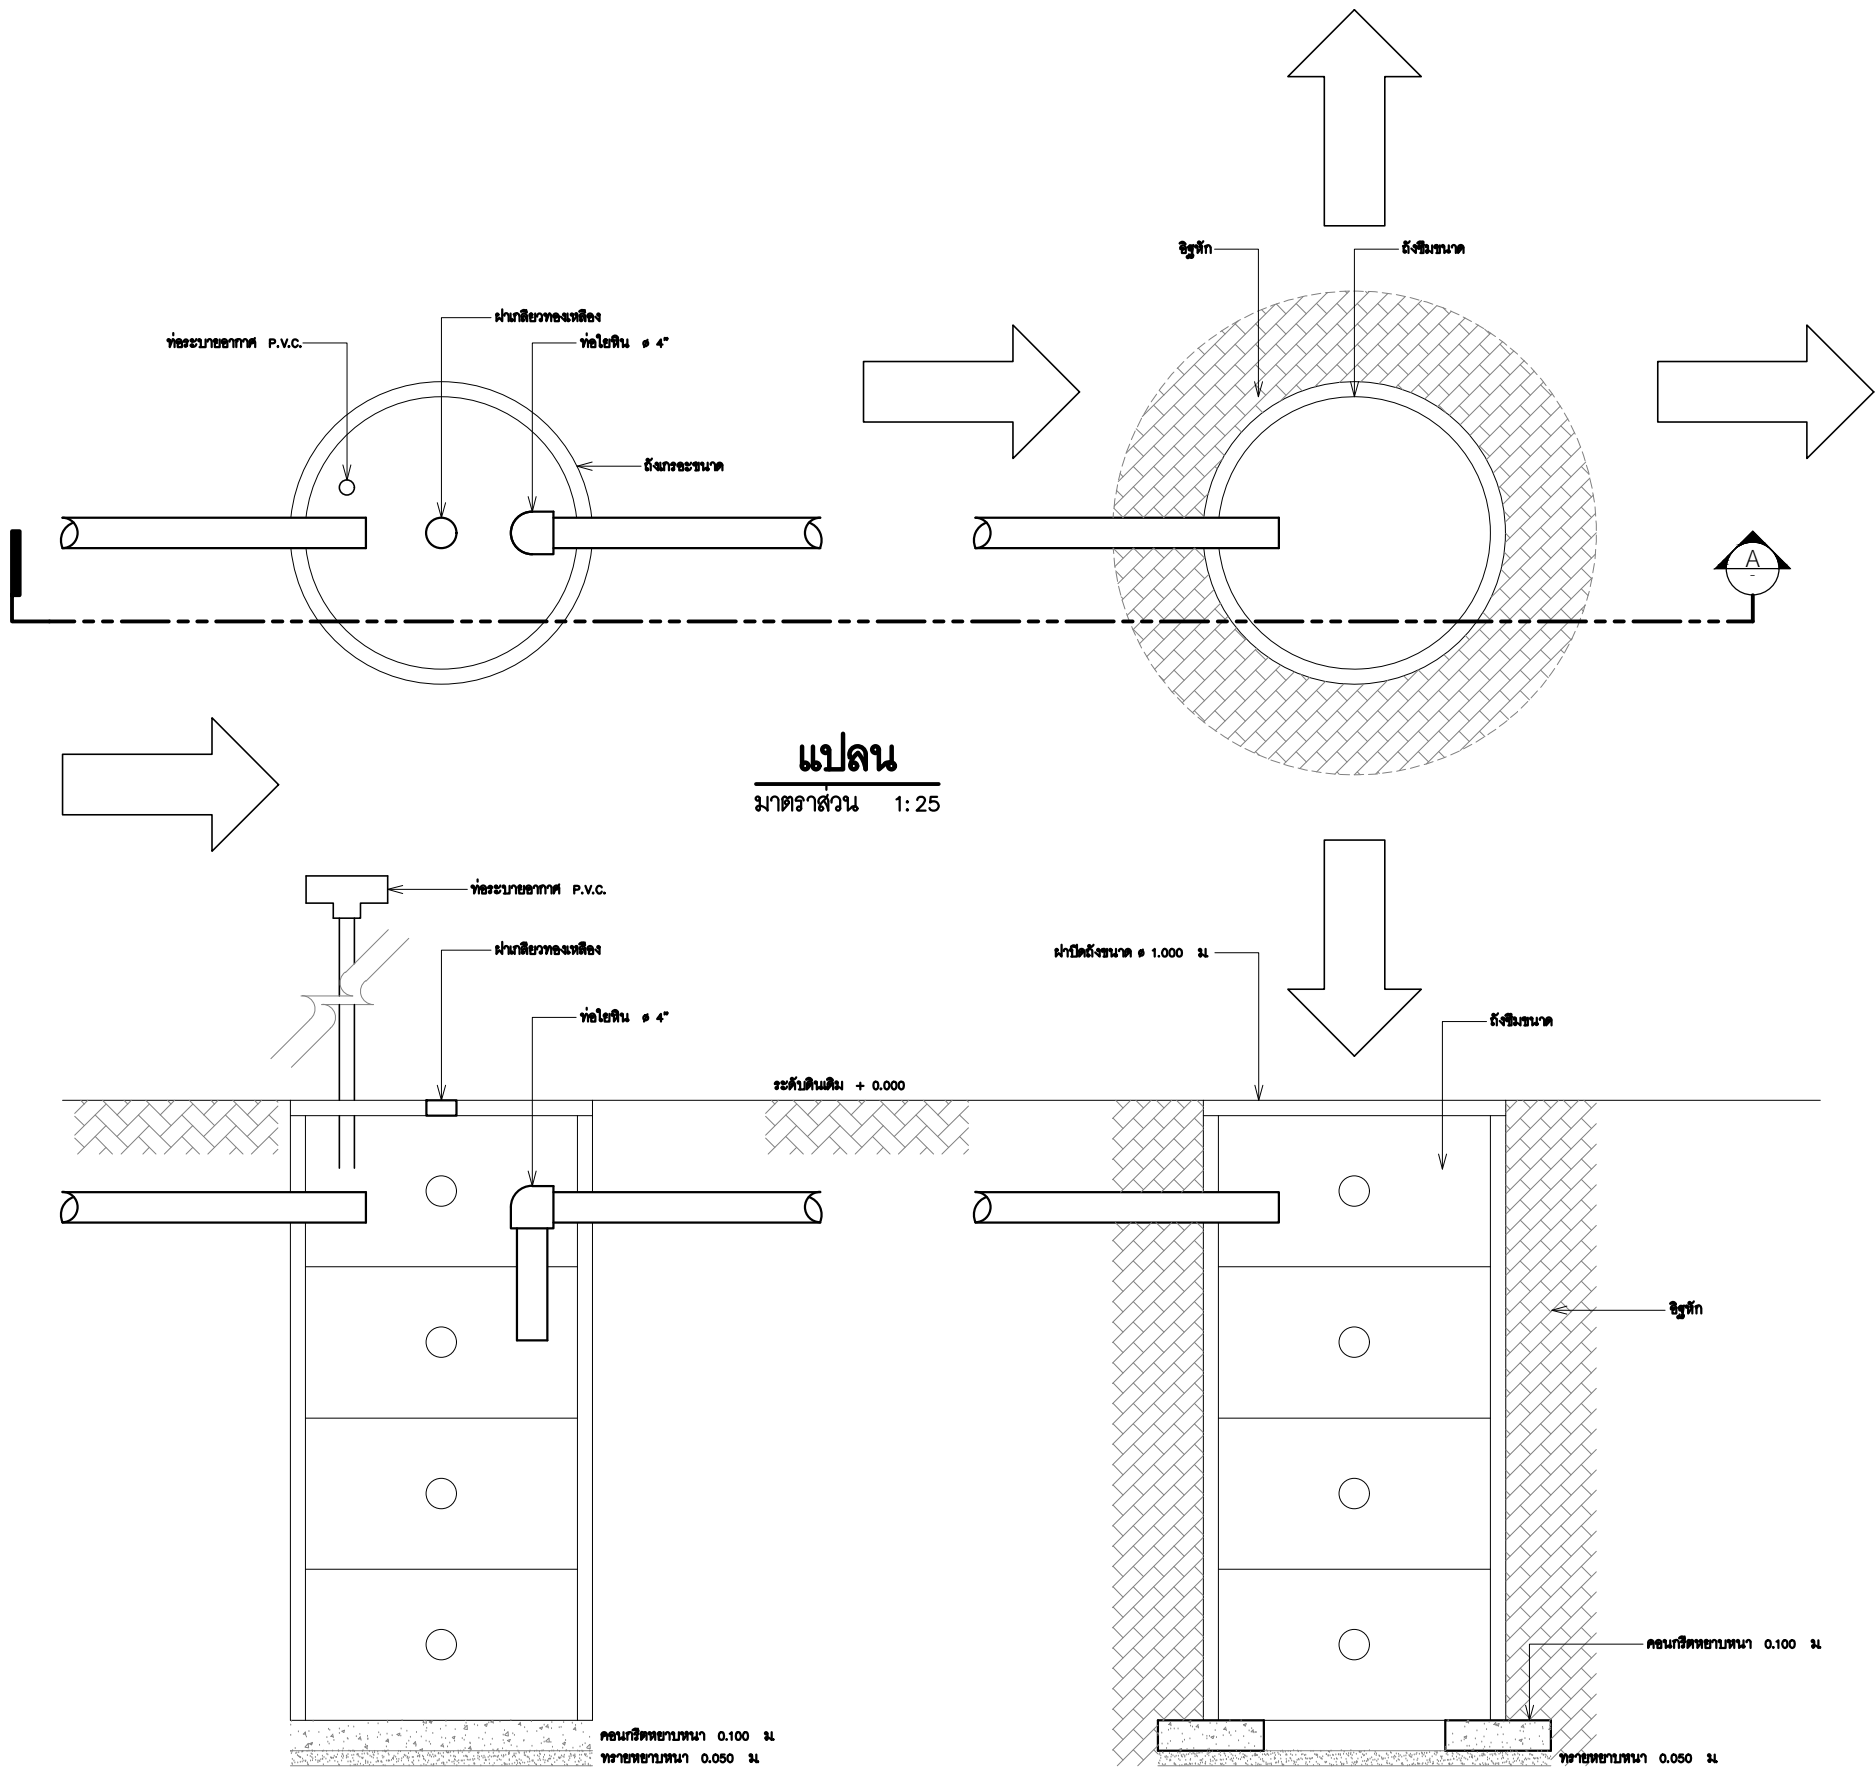


แปลน
มาตราส่วน 1:25

รูปตัด A
มาตราส่วน 1:25

แบบขยายบ่อเกรอะ-บ่อซึม
มาตราส่วน 1:25


PROJECT NAME						
สำนักงานนิติบุคคลหมู่บ้านจัดสรร พฤษา 33						
LOCATION						
ตำบลบางแม่นาง						
อำเภอบางใหญ่ จังหวัดนนทบุรี						
OWNER						
นิติบุคคลหมู่บ้านจัดสรรพฤษา33						
ARCHITECTS						
-						
-						
-						
ENGINEERS						
-						
-						
-						
TITLE						
แบบขยายบ่อเกรอะ-บ่อซึม						
REVISION						
1	2	3	4	5	6	7
DRAWN BY						
-						
-						
DATE	2025-09-01					
DRAWING NO.	TOTAL					
SN-03	OF					

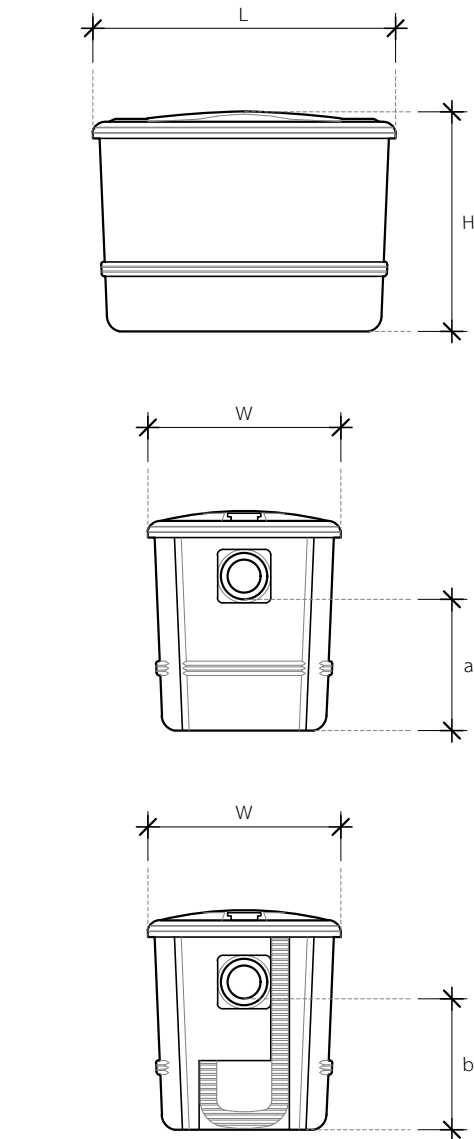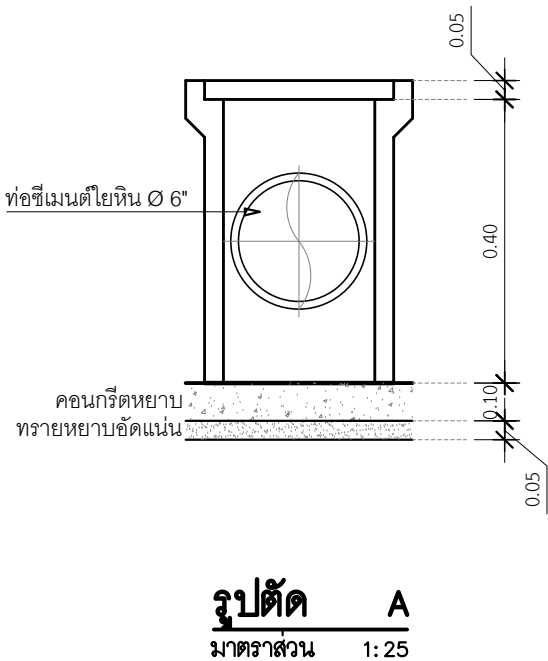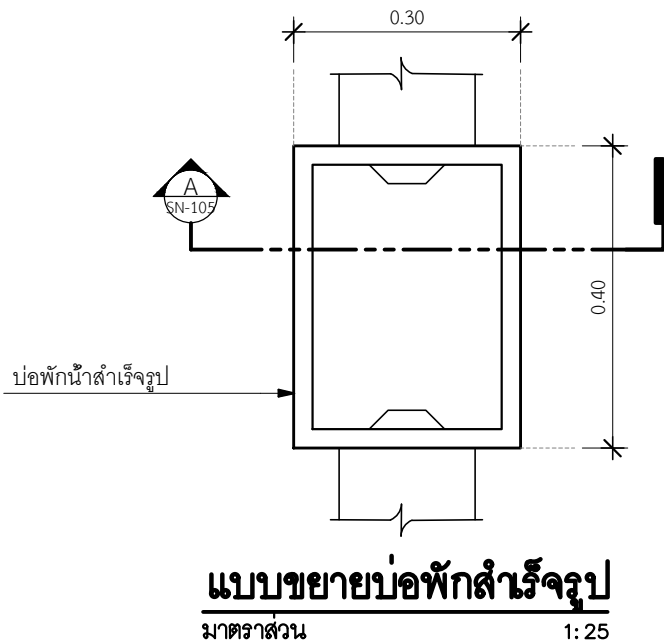

G-TEK	กว้าง W : cm.	ลึก L : cm.	สูง H : cm.	ขนาดเส้นผ่าศูนย์กลางท่อ			
				ท่อเข้า	ท่อออก	ท่อระบายไขมัน	ท่อระบายตะกอน
15 L	29	47	33	2"	2"	1"	3/4"
40 L	39	57	42	2"	2"	1"	3/4"

ขนาดถังดักไขมัน ยี่ห้อ DOS | รุ่น G-TEK

แบบขยายถังดักไขมัน

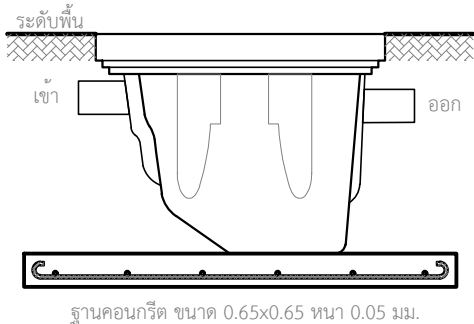

การติดตั้งถังดักไขมัน

PROJECT NAME						
สำนักงานนิติบุคคลหมู่บ้านจัดสรร พฤษา 33						
LOCATION						
ตำบลบางแม่นาง						
อำเภอบางใหญ่ จังหวัดนนทบุรี						
OWNER						
นิติบุคคลหมู่บ้านจัดสรรพฤษา33						
ARCHITECTS						
-						
-						
-						
ENGINEERS						
-						
-						
-						
TITLE						
แบบขยายบ่อพักสำเร็จรูป						
แบบขยายถังดักไขมัน และ การติดตั้ง						
REVISION						
1	2	3	4	5	6	7
DRAWN BY						
-						
-						
DATE	2025-09-01					
DRAWING NO.	TOTAL					
SN-04	OF					